



Asphalt Road


NOTES:-

- (1) THIS DRAWING IS THE PROPERTY OF :
BARAJEEL ENGINEERING CONSULTANTS
P.O.BOX 14496, DUBAI, U.A.E.
IT IS NOT ALLOWED TO REPRODUCE ITS CONTENTS
IN ANY FORM EXCEPT FOR THE PURPOSE FOR
WHICH IT IS NEEDED.
 - (2) THIS DRAWING IS NOT TO BE SCALED. STATED
DIMENSIONS ONLY ARE TO BE CONSIDERED.
 - (3) ANY DISCREPANCIES ARE TO BE BROUGHT TO
THE ATTENTION OF THE ENGINEER AND RESOLVED
BEFORE COMMENCEMENT OF ANY WORK.
 - (4) ALL DIMENSIONS ARE IN CENTIMETERS.

No:	DESCRIPTION		DATE	SIGN
PLOT:	LOCATION:			
JVC10WMRM001	JUMEIRA VILLAGE CIRCLE			
CLIENT: KARIM MIRZAAGHA JAHED PARI				
CONSULTANT:  AL GAFRY الغافري <small>CONSULTING ARCHITECTS ENGINEERS P.O.BOX NO:-48347,Dubai,U.A.E TELE:-+971 42678181,FAX NO:-+971 42671881</small>				
CONTRACTOR: <input checked="" type="checkbox"/> ZENITH SMART CONTRACTING AL SHAFAR TOWER 1,TECOM BARSHA,DUBAI-P.O.BOX.125180 P.O.Box:125180 DUBAI. Tel: 043688588 FAX:043688424				
PROJECT: Proposed Residential & Commercial Building Gr. + 3P. + 11 Floor + ROOF PLOT NO: JVC10WMRM001, AL BARSHA SOUTH FOURTH				
STAGE: ARCHITECTURAL				
DRAWING TITLE: SETTING OUT PLAN				
CAD FILE:				
SCALE	DATE	DRAWN BY	JOB NO.	
N.T.S	DEC/2024			



UNDERGROUND STRUCTURE DETAILS

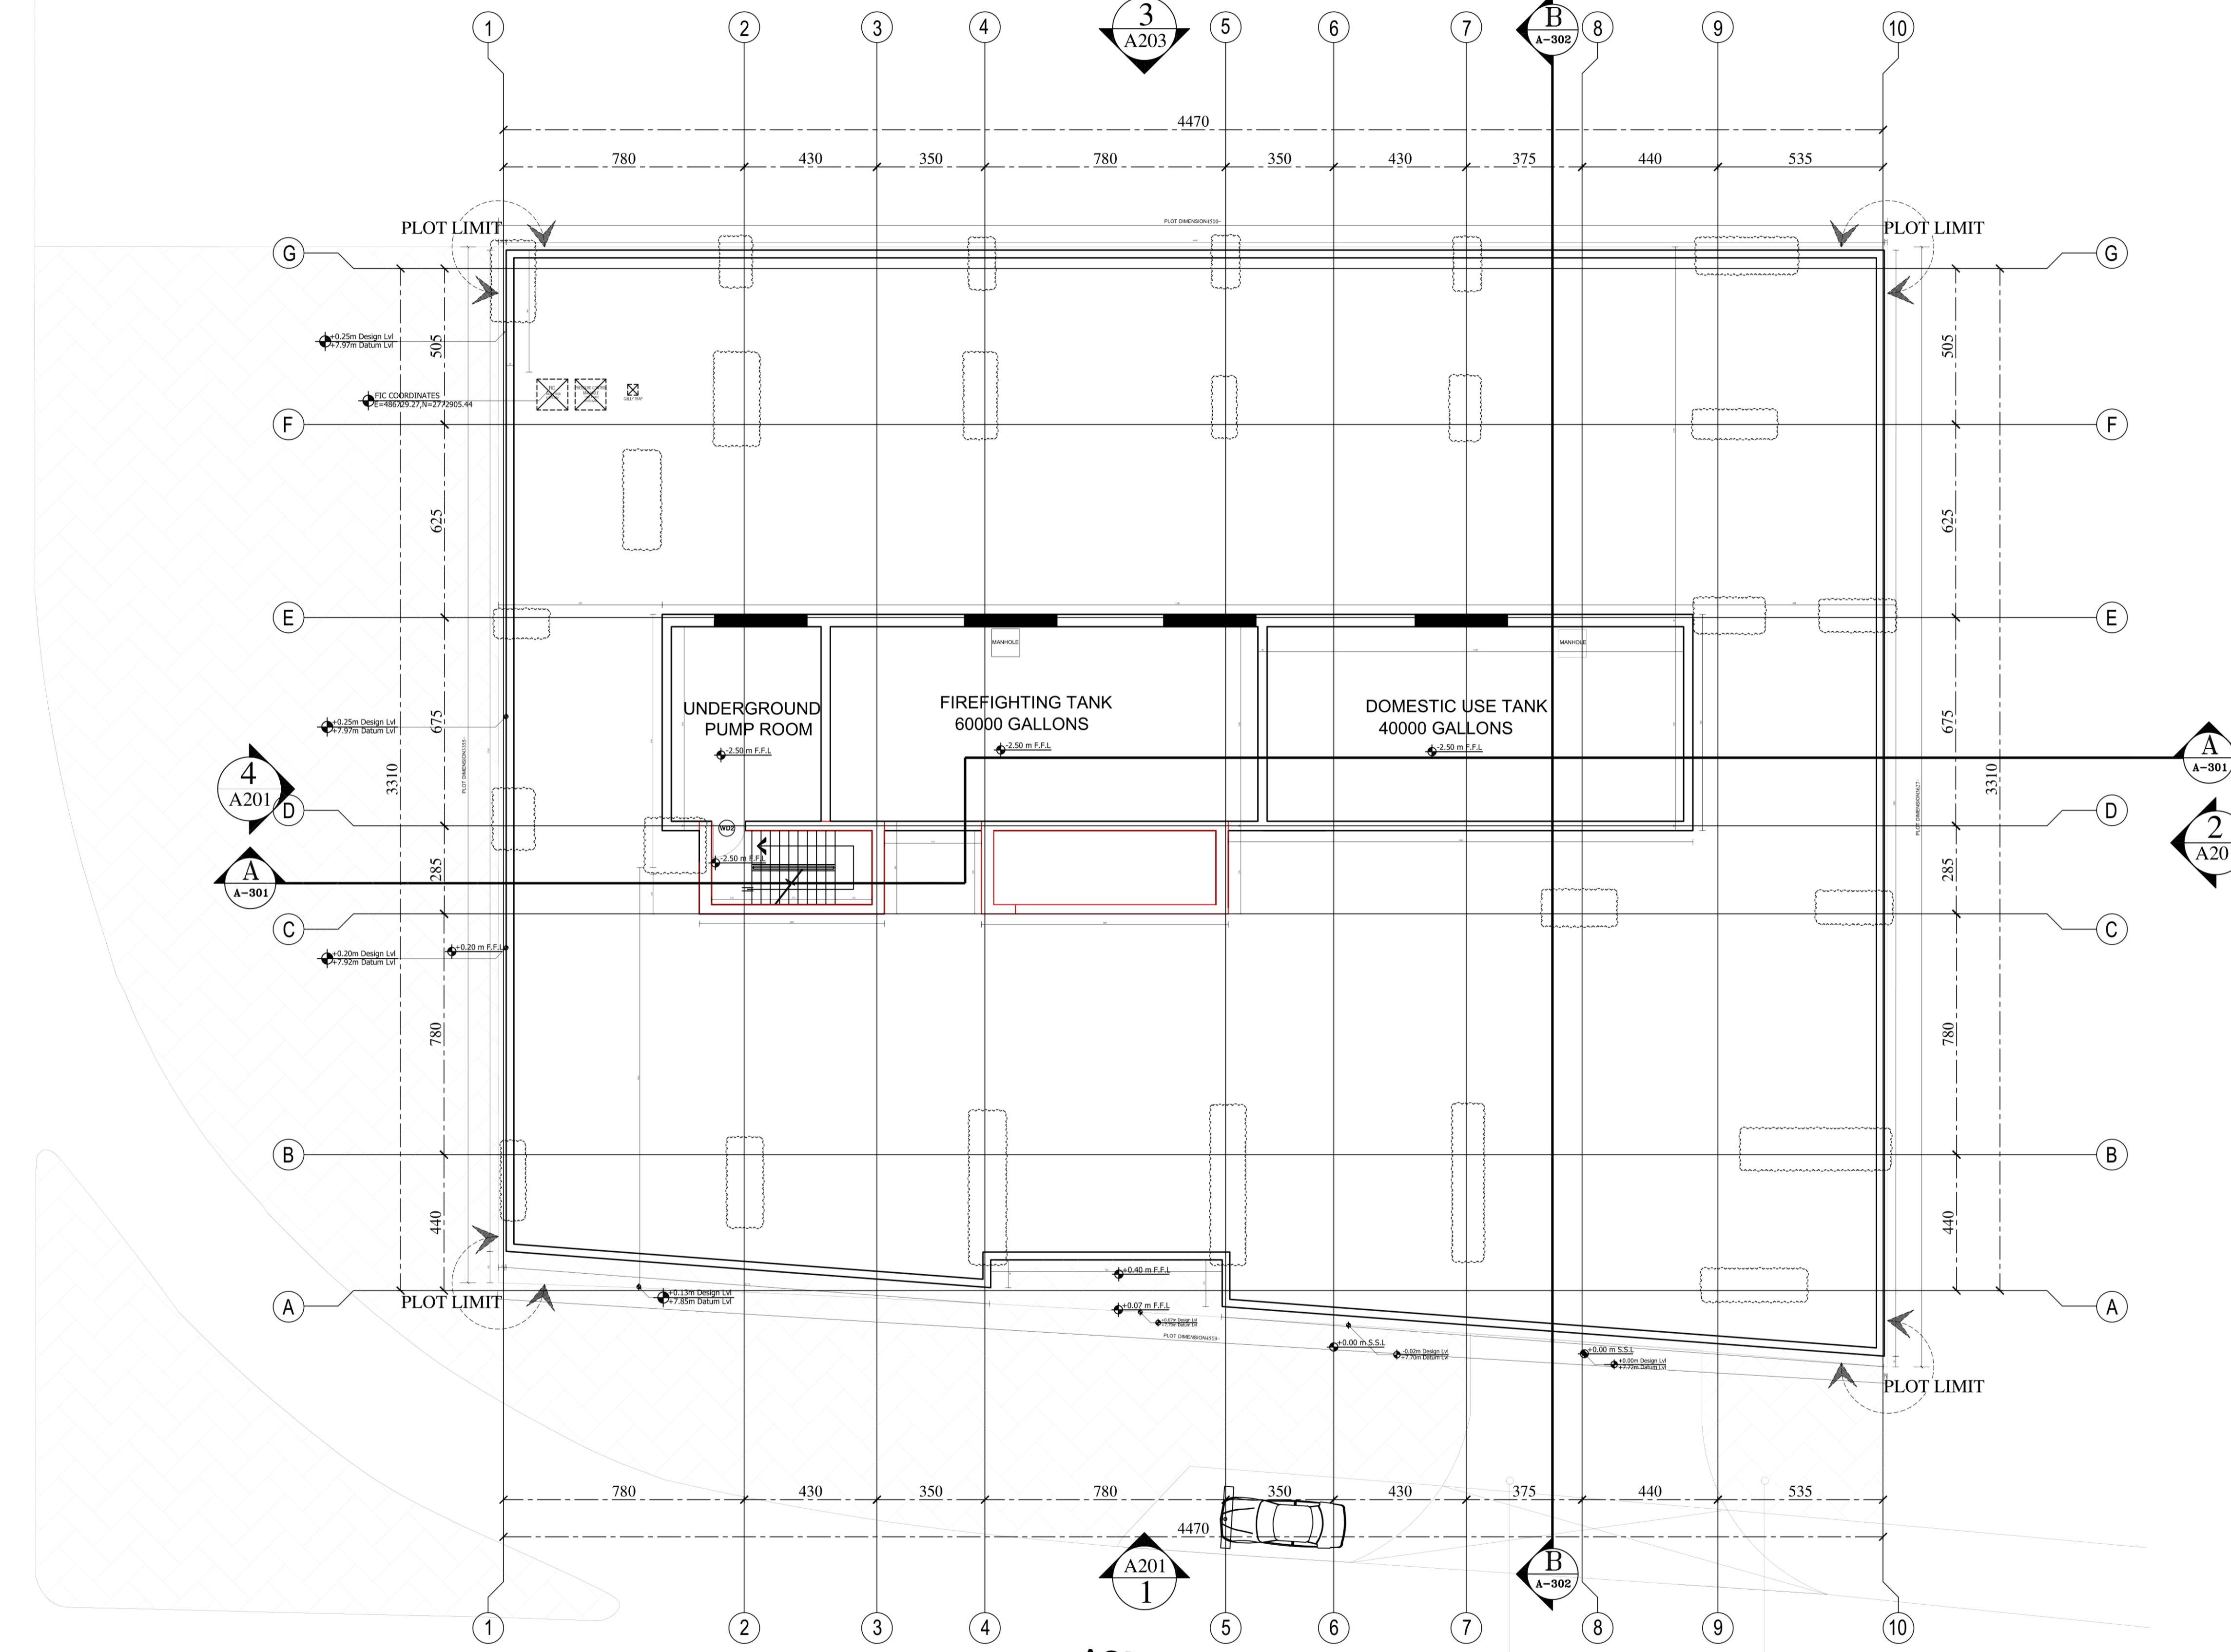

NOTES:-

- (1) THIS DRAWING IS THE PROPERTY OF :
BARAJEEL ENGINEERING CONSULTANTS
P.O.BOX 14496, DUBAI, U.A.E.
IT IS NOT ALLOWED TO REPRODUCE ITS CONTENTS
IN ANY FORM EXCEPT FOR THE PURPOSE FOR
WHICH IT IS NEEDED.
 - (2) THIS DRAWING IS NOT TO BE SCALED. STATED
DIMENSIONS ONLY ARE TO BE CONSIDERED.
 - (3) ANY DISCREPANCIES ARE TO BE BROUGHT TO
THE ATTENTION OF THE ENGINEER AND RESOLVED
BEFORE COMMENCEMENT OF ANY WORK.
 - (4) ALL DIMENSIONS ARE IN CENTIMETERS.

PLOT: LOCATION:
JVC10WMRM001 JUMEIRA VILLAGE CIRCLE

CLIENT: KARTIM MIRZAAGHA JAHED PART

CONTRACTOR:

ZENITH SMART CONTRACTING
AL SHAFAR TOWER 1,TECOM
BARSHA,DUBAI-P.O.BOX.125180
P.O.Box:125180, DUBAI, Tel: 043688588, FAX:043688424


PROJECT:
Proposed Residential & Commercial Building
Gr. + 3P. + 11 Floor + ROOF
PLOT NO: JVC10WMRM001, AL BARSHA SOUTH FOURTH

STAGE: ARCHITECTURAL

DRAWING TITLE:

CAD FILE:

SCALE	DATE	DRAWN BY	JOB NO.	
N.T.S	DEC/2024			

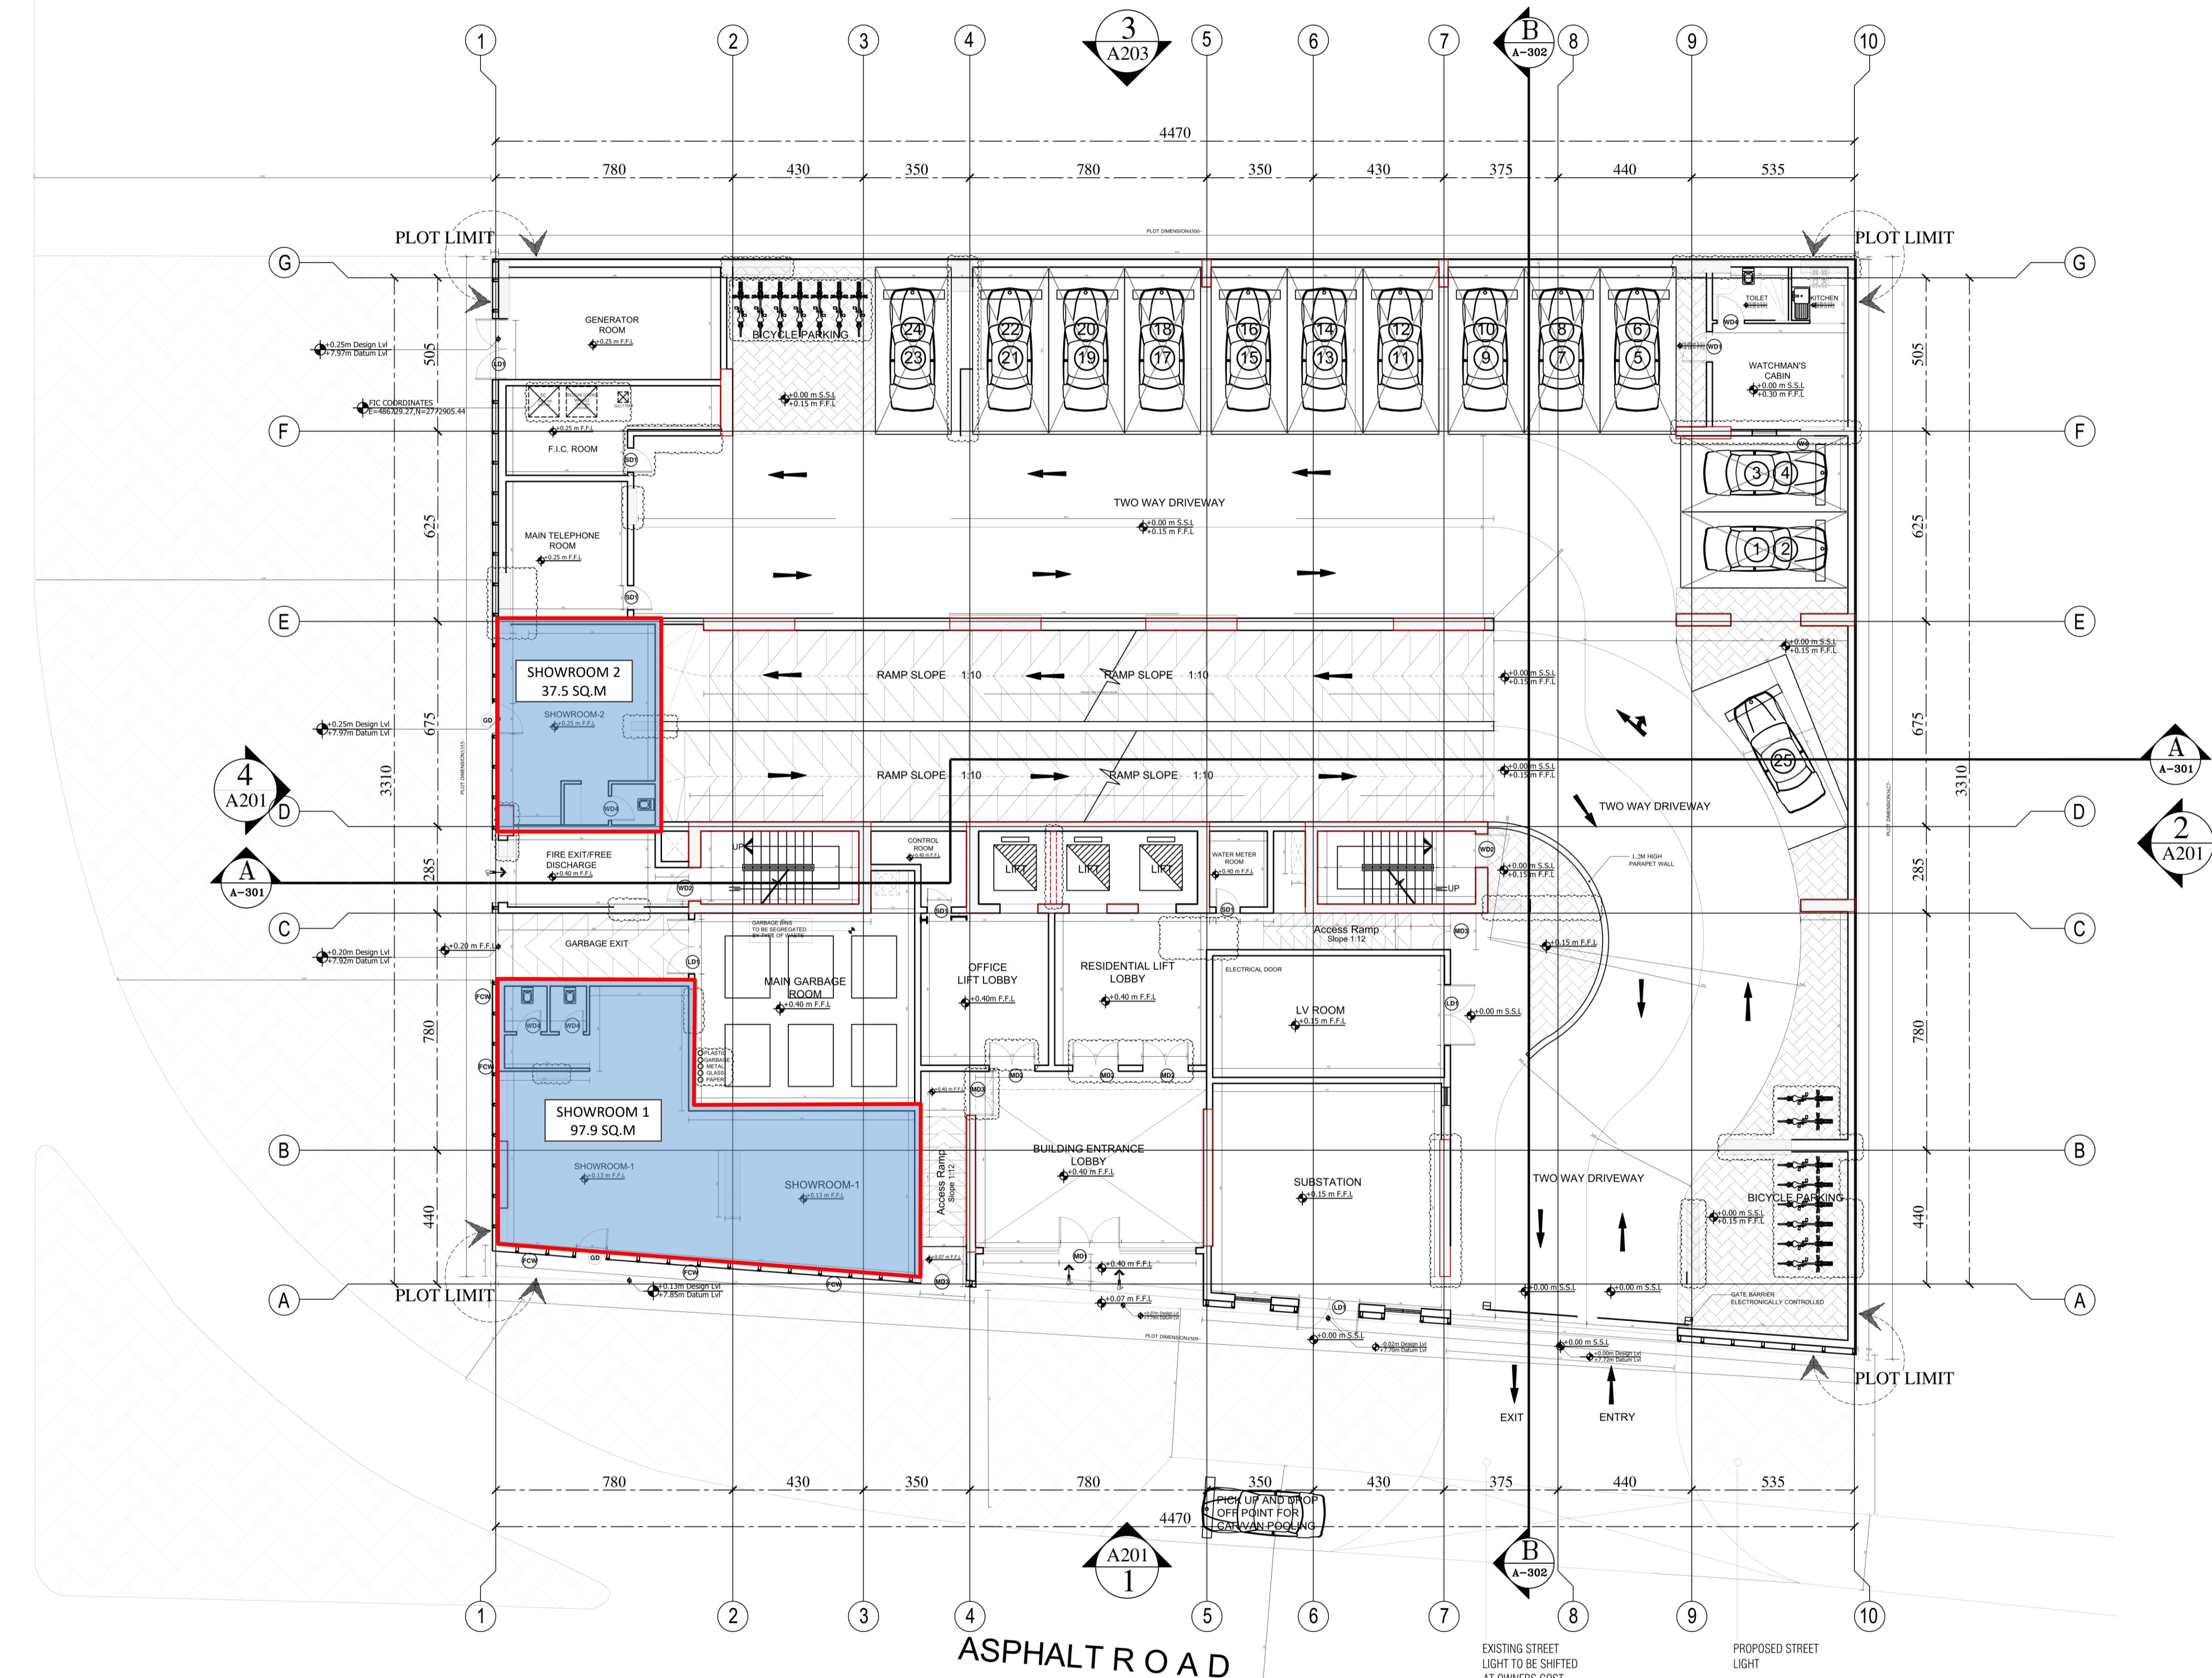

SELLABLE AREA	
SHOWROOM-1 : 97.9 SQ.M	
SHOWROOM-2 : 37.5 SQ.M	

GROUND FLOOR

No:	DESCRIPTION	DATE	SIGN
PLOT: JVC10WMR001 LOCATION: JUMEIRA VILLAGE CIRCLE			
CLIENT: KARIM MIRZAAGHA JAHED PARI			
CONSULTANT: AL GAFRY			
 CONSULTING ARCHITECTS ENGINEERS P.O.BOX NO-48347,Dubai,U.A.E TEL:-+971 42678184,FAX NO.-971 42671881			
CONTRACTOR: ZENITH SMART CONTRACTING			
AL SHAFAR TOWER 1,TECOM BARSHA,DUBAI-P.O.BOX.125180 P.O.Box:125180 DUBAI Tel: 043688588 FAX:043688424			
PROJECT: Proposed Residential & Commercial Building			
Gr. + 3P. + 11 Floor + ROOF			
PLOT NO: JVC10WMR001, AL BARSHA SOUTH FOURTH			
STAGE: ARCHITECTURAL			
DRAWING TITLE: GROUND FLOOR PLAN			
CAD FILE:			
SCALE	DATE	DRAWN BY	JOB NO.
N.T.S	DEC/2024		



NOTES:-

(1) THIS DRAWING IS THE PROPERTY OF :
BARAJEEL ENGINEERING CONSULTANTS
P.O.BOX 14496, DUBAI, U.A.E.
IT IS NOT ALLOWED TO REPRODUCE ITS CONTENTS
IN ANY FORM EXCEPT FOR THE PURPOSE FOR
WHICH IT IS NEEDED.

(2) THIS DRAWING IS NOT TO BE SCALED. STATED
DIMENSIONS ONLY ARE TO BE CONSIDERED.

(3) ANY DISCREPANCIES ARE TO BE BROUGHT TO
THE ATTENTION OF THE ENGINEER AND RESOLVED
BEFORE COMMENCEMENT OF ANY WORK.


(4) ALL DIMENSIONS ARE IN CENTIMETERS.


No:	DESCRIPTION	DATE	SIGN
PLOT:	LOCATION:		
JVC10WMRM001	JUMEIRA VILLAGE CIRCLE		
CLIENT: KARIM MIRZAAGHA JAHED PARI			
CONSULTANT:  AL GAFRY الغافري <small>CONSULTING ARCHITECTS ENGINEERS P.O.BOX NO:-48347,Dubai,U.A.E TELE:-+971 42678181,FAX NO:-+971 42671881</small>			
CONTRACTOR: <input checked="" type="checkbox"/> ZENITH SMART CONTRACTING AL SHAFAR TOWER 1,TECOM BARSHA,DUBAI-P.O.BOX.125180 P.O.Box:125180 DUBAI. Tel: 043688588 FAX:043688424			
PROJECT: Proposed Residential & Commercial Building Gr. + 3P. + 11 Floor + ROOF PLOT NO: JVC10WMRM001, AL BARSHA SOUTH FOURTH			
STAGE: ARCHITECTURAL			
DRAWING TITLE: PODIUM 1			
CAD FILE:			
SCALE	DATE	DRAWN BY	JOB NO.
N.T.S	DEC/2024		



NOTES:-

- (1) THIS DRAWING IS THE PROPERTY OF :
BARAJEEL ENGINEERING CONSULTANTS
P.O.BOX 14496, DUBAI, U.A.E.
IT IS NOT ALLOWED TO REPRODUCE ITS CONTENTS
IN ANY FORM EXCEPT FOR THE PURPOSE FOR
WHICH IT IS NEEDED.
 - (2) THIS DRAWING IS NOT TO BE SCALED. STATED
DIMENSIONS ONLY ARE TO BE CONSIDERED.
 - (3) ANY DISCREPANCIES ARE TO BE BROUGHT TO
THE ATTENTION OF THE ENGINEER AND RESOLVED
BEFORE COMMENCEMENT OF ANY WORK.
 - (4) ALL DIMENSIONS ARE IN CENTIMETERS.

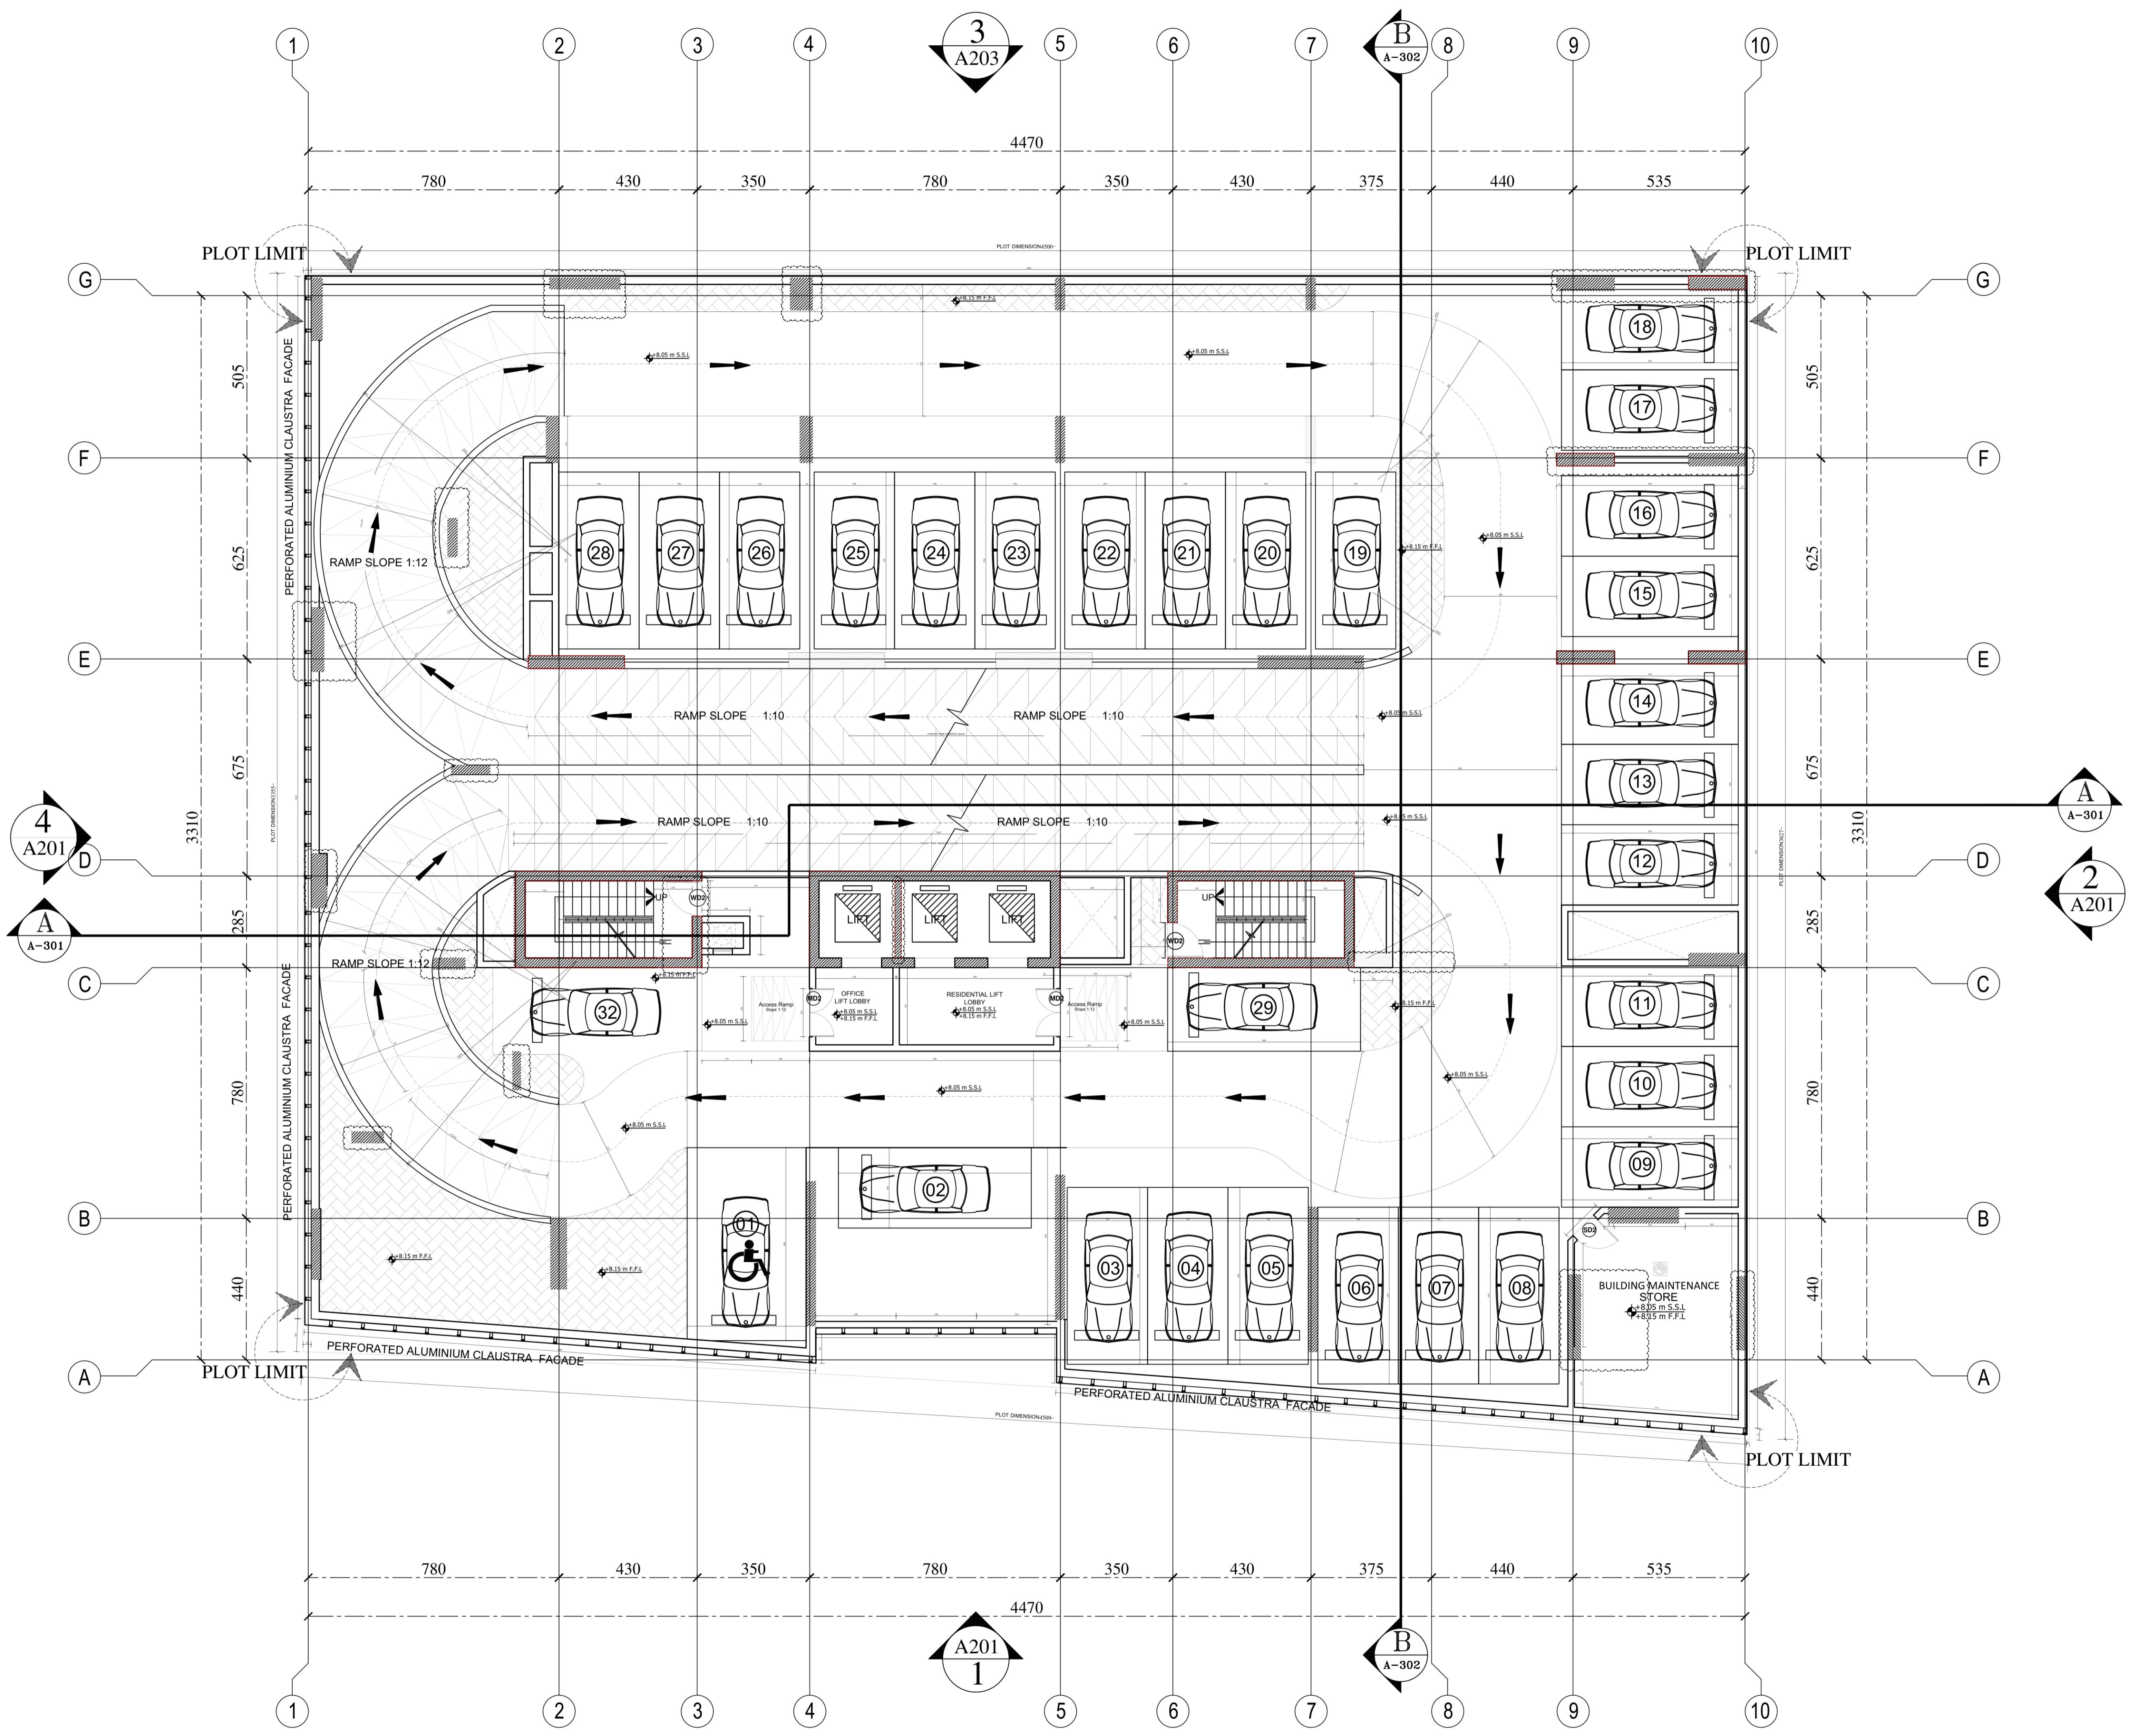

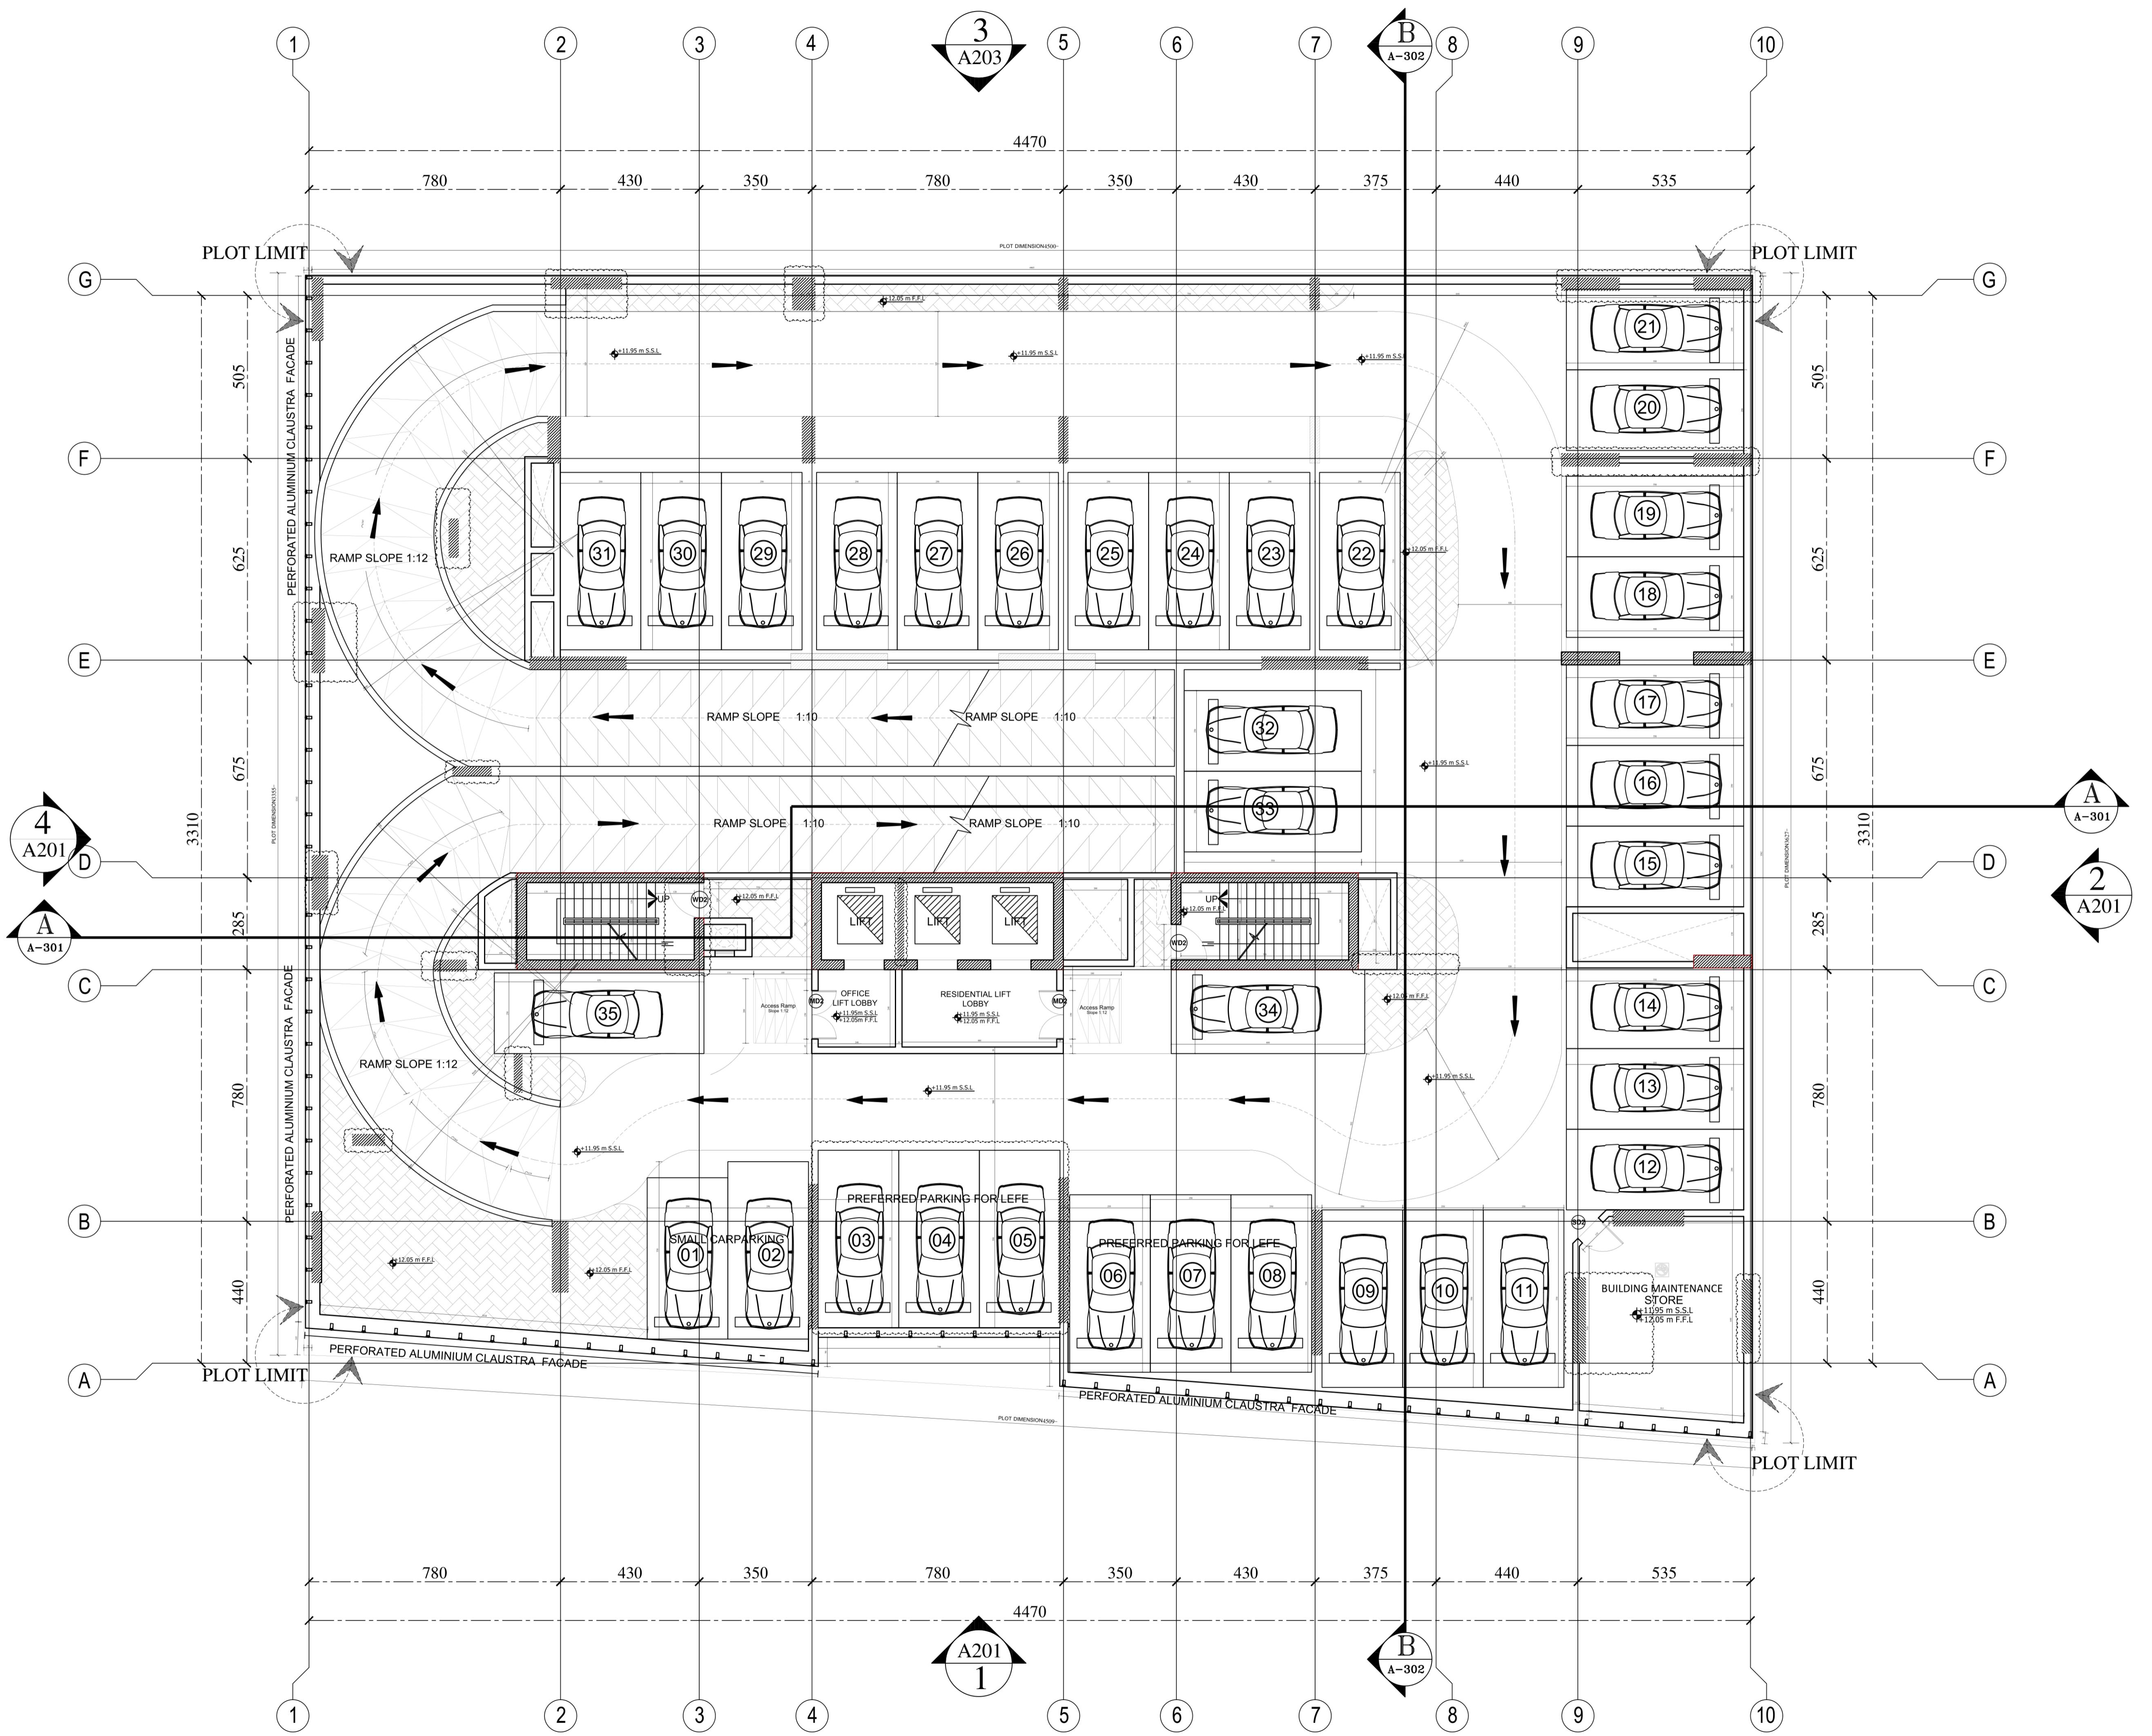



NOTES:-

(1) THIS DRAWING IS THE PROPERTY OF :
BARAJEEL ENGINEERING CONSULTANTS
P.O.BOX 14496, DUBAI, U.A.E.
IT IS NOT ALLOWED TO REPRODUCE ITS CONTENTS
IN ANY FORM EXCEPT FOR THE PURPOSE FOR
WHICH IT IS NEEDED.

(2) THIS DRAWING IS NOT TO BE SCALED. STATED
DIMENSIONS ONLY ARE TO BE CONSIDERED.

(3) ANY DISCREPANCIES ARE TO BE BROUGHT TO
THE ATTENTION OF THE ENGINEER AND RESOLVED
BEFORE COMMENCEMENT OF ANY WORK.


(4) ALL DIMENSIONS ARE IN CENTIMETERS.

No:	DESCRIPTION		DATE	SIGN
PLOT:		LOCATION:		
JVC10WMRM001		JUMEIRA VILLAGE CIRCLE		
CLIENT: KARIM MIRZAAGHA JAHED PARI				
CONSULTANT:  AL GAFRY الغافري CONSULTING ARCHITECTS ENGINEERS P.O.BOX NO:-48347,Dubai,U.A.E TELE:-+971 42678181,FAX NO:-+971 42671881				
CONTRACTOR: <input checked="" type="checkbox"/> ZENITH SMART CONTRACTING AL SHAFAR TOWER 1,TECOM BARSHA,DUBAI-P.O.BOX.125180 P.O.Box:125180 DUBAI. Tel: 043688588 FAX:043688424				
PROJECT: Proposed Residential & Commercial Building Gr. + 3P. + 11 Floor + ROOF PLOT NO: JVC10WMRM001, AL BARSHA SOUTH FOURTH				
STAGE: ARCHITECTURAL				
DRAWING TITLE: FIRST FLOOR OFFICE				
CAD FILE:				
SCALE	DATE	DRAWN BY	JOB NO.	
N.T.S	DEC/2024			



NOTES:-

- (1) THIS DRAWING IS THE PROPERTY OF : BARAJEEL ENGINEERING CONSULTANTS P.O.BOX 14496, DUBAI, U.A.E. IT IS NOT ALLOWED TO REPRODUCE ITS CONTENTS IN ANY FORM EXCEPT FOR THE PURPOSE FOR WHICH IT IS NEEDED.
- (2) THIS DRAWING IS NOT TO BE SCALED. STATED DIMENSIONS ONLY ARE TO BE CONSIDERED.
- (3) ANY DISCREPANCIES ARE TO BE BROUGHT TO THE ATTENTION OF THE ENGINEER AND RESOLVED BEFORE COMMENCEMENT OF ANY WORK.
- (4) ALL DIMENSIONS ARE IN CENTIMETERS.

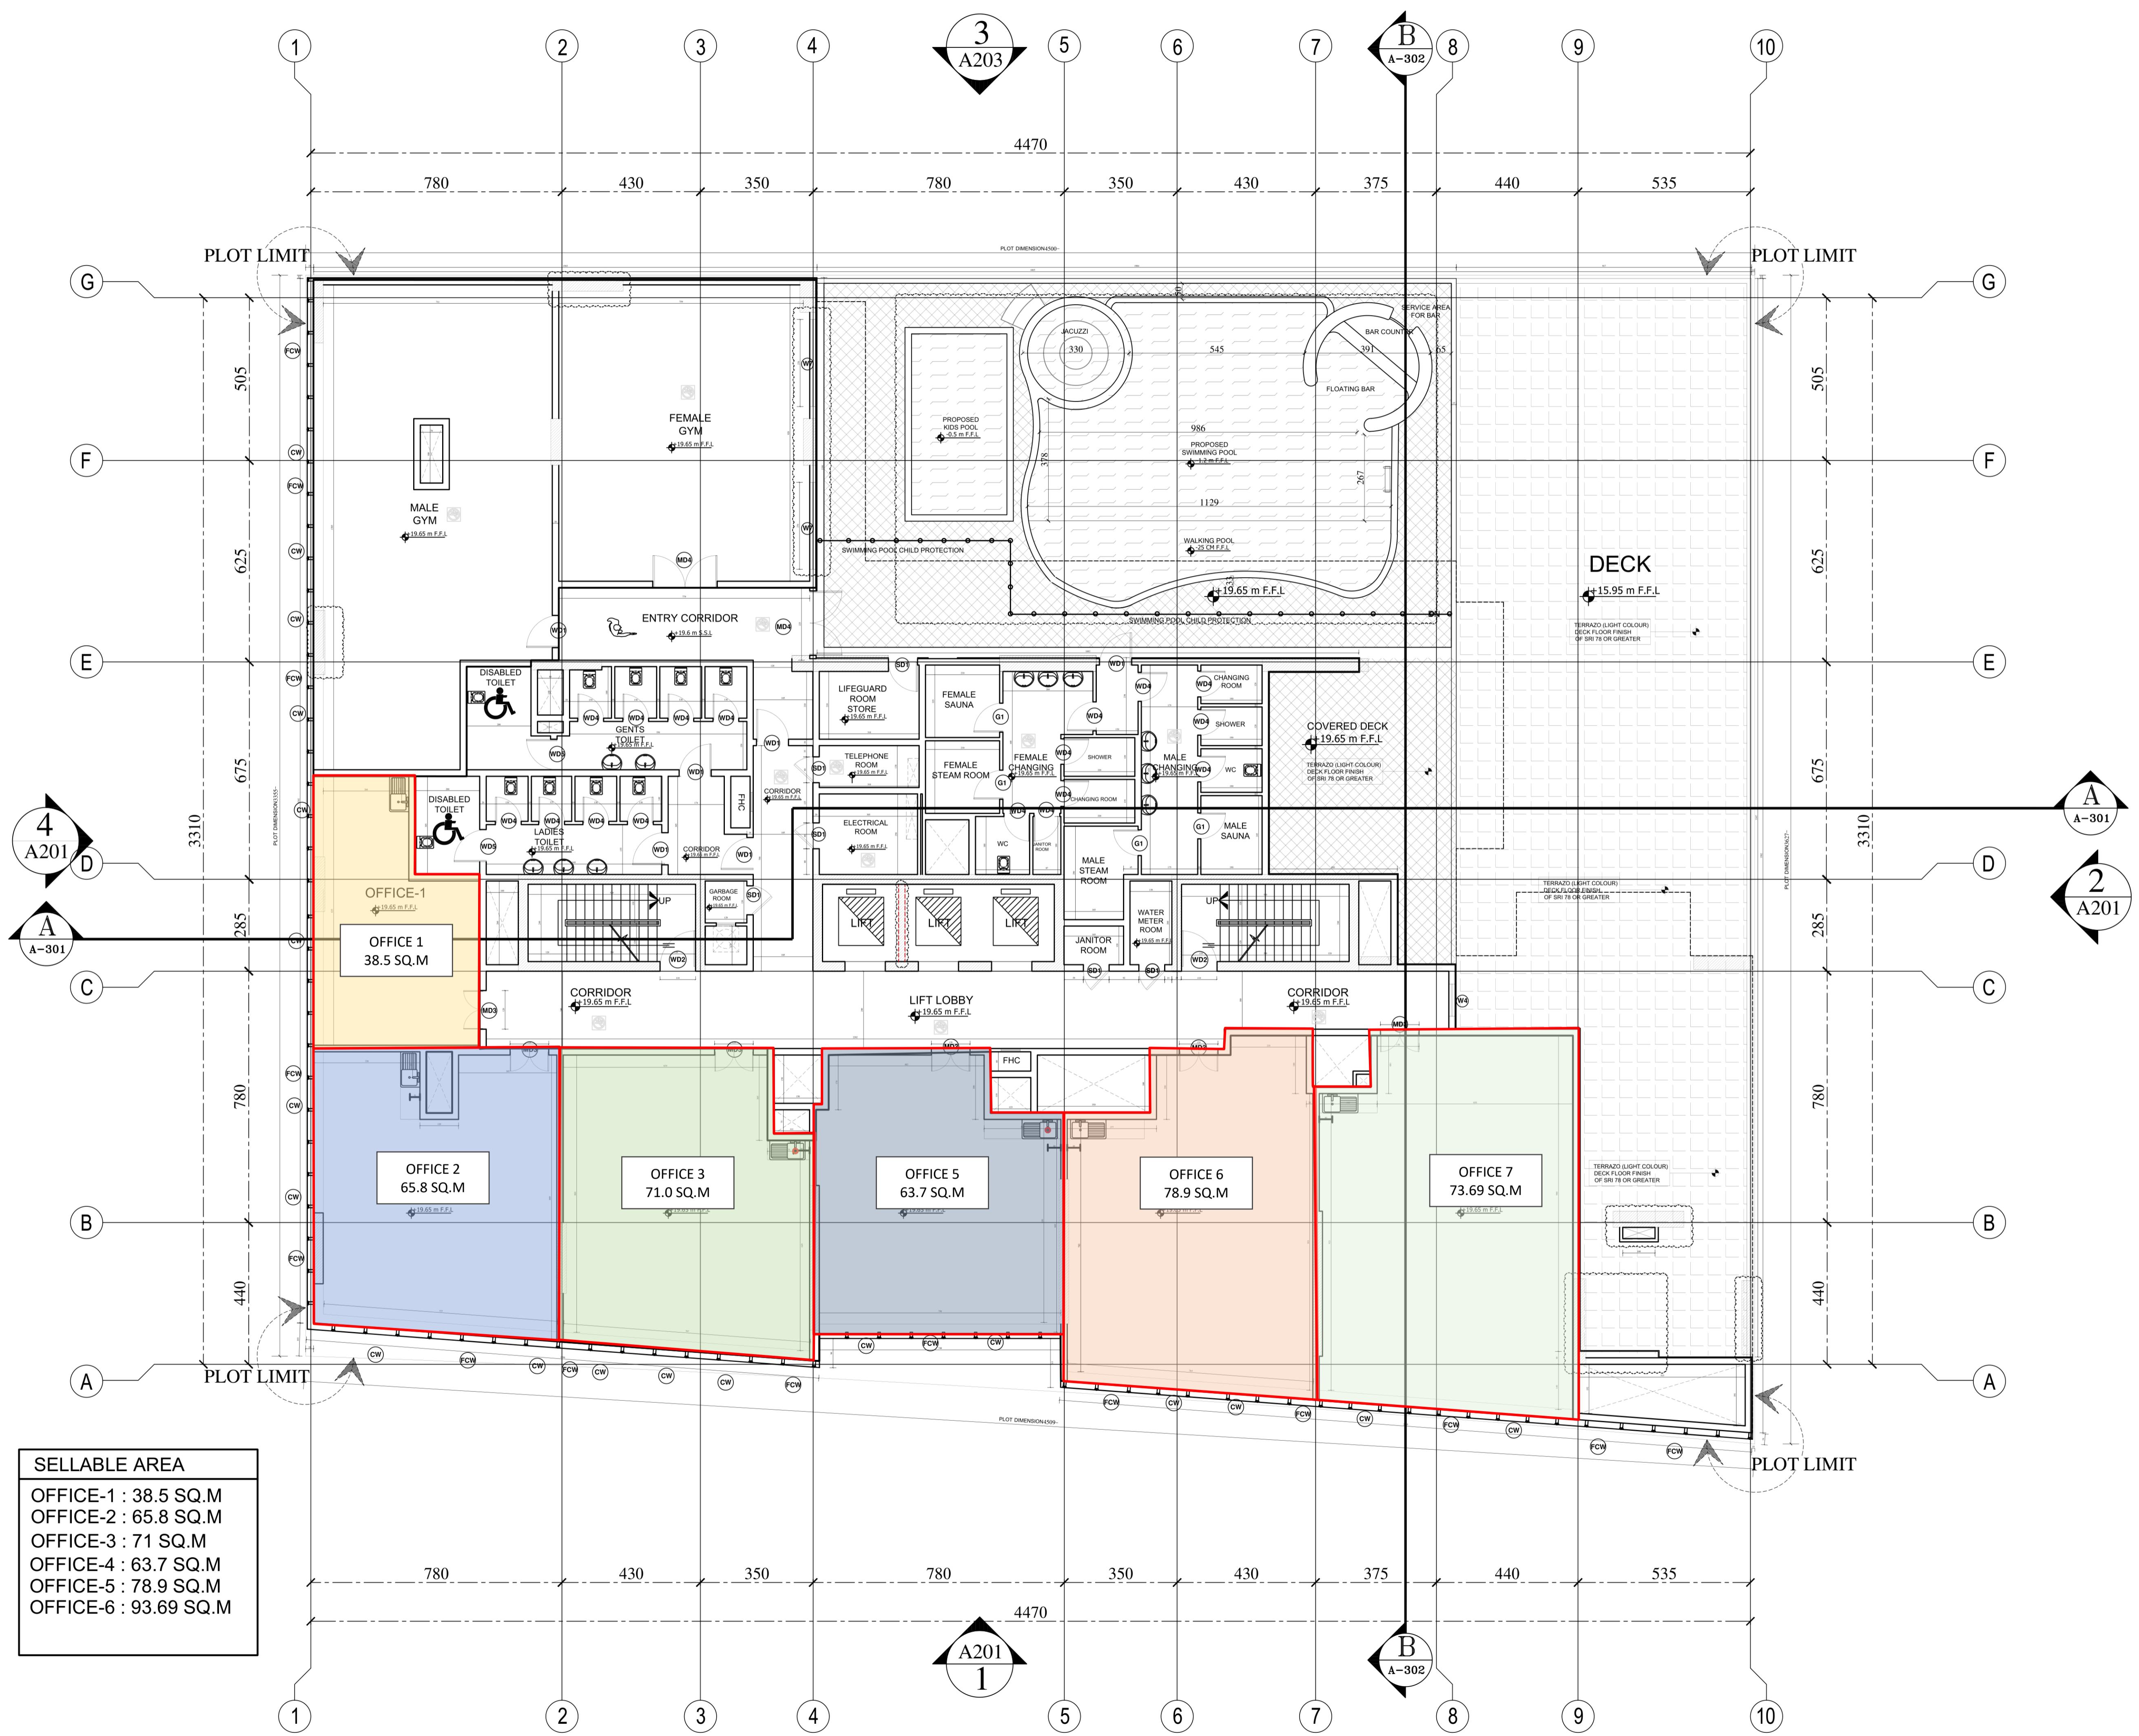


No:	DESCRIPTION	DATE	SIGN
PLOT: JVC10WMR001 LOCATION: JUMEIRA VILLAGE CIRCLE			
CLIENT: KARIM MIRZAAGHA JAHED PARI			
CONSULTANT: AL GAFRY			
AL GAFRY <small>CONSULTING ARCHITECTS ENGINEERS P.O.BOX NO-48347,Dubai,U.A.E TELE:-+971 42678184,FAX NO.-+971 42671881</small>			
CONTRACTOR: <input checked="" type="checkbox"/> ZENITH SMART CONTRACTING			
ZENITH SMART CONTRACTING <small>AL SHAFAR TOWER 1,TECOM BARSHA,DUBAI-P.O.BOX.125180 P.O.Box:125180 DUBAI Tel: 043688588 FAX:043688424</small>			
PROJECT: Proposed Residential & Commercial Building Gr. + 3P. + 11 Floor + ROOF			
PLOT NO: JVC10WMR001, AL BARSHA SOUTH FOURTH			
STAGE: ARCHITECTURAL			
DRAWING TITLE: SECOND FLOOR OFFICE+GYM			
CAD FILE:			
SCALE	DATE	DRAWN BY	JOB NO.
N.T.S	DEC/2024		



NOTES:-

- (1) THIS DRAWING IS THE PROPERTY OF :
BARAJEEL ENGINEERING CONSULTANTS
P.O.BOX 14496, DUBAI, U.A.E.
IT IS NOT ALLOWED TO REPRODUCE ITS CONTENTS
IN ANY FORM EXCEPT FOR THE PURPOSE FOR
WHICH IT IS NEEDED.
- (2) THIS DRAWING IS NOT TO BE SCALED. STATED
DIMENSIONS ONLY ARE TO BE CONSIDERED.
- (3) ANY DISCREPANCIES ARE TO BE BROUGHT TO
THE ATTENTION OF THE ENGINEER AND RESOLVED
BEFORE COMMENCEMENT OF ANY WORK.
- (4) ALL DIMENSIONS ARE IN CENTIMETERS.


No:	DESCRIPTION	DATE	SIGN
PLOT:	LOCATION:		
JVC10WMRM001	JUMEIRA VILLAGE CIRCLE		
CLIENT:			
KARIM MIRZAAGHA JAHED PARI			
CONSULTANT:			
 AL GAFRY الغافري <small>CONSULTING ARCHITECTS ENGINEERS P.O.BOX NO:-48347,Dubai,U.A.E TELE:-+971 42678181,FAX NO:-+971 42671881</small>			
CONTRACTOR:			
<input checked="" type="checkbox"/> ZENITH SMART CONTRACTING AL SHAFAR TOWER 1,TECOM BARSHA,DUBAI-P.O.BOX.125180 <small>P.O.Box:125180 DUBAI. Tel: 043688588 FAX:043688424</small>			
PROJECT:			
Proposed Residential & Commercial Building Gr. + 3P. + 11 Floor + ROOF PLOT NO: JVC10WMRM001, AL BARSHA SOUTH FOURTH			
STAGE: ARCHITECTURAL			
DRAWING TITLE:			
THIRD FLOOR RESIDENTIAL			
CAD FILE:			
SCALE	DATE	DRAWN BY	JOB NO.
N.T.S	DEC/2024		

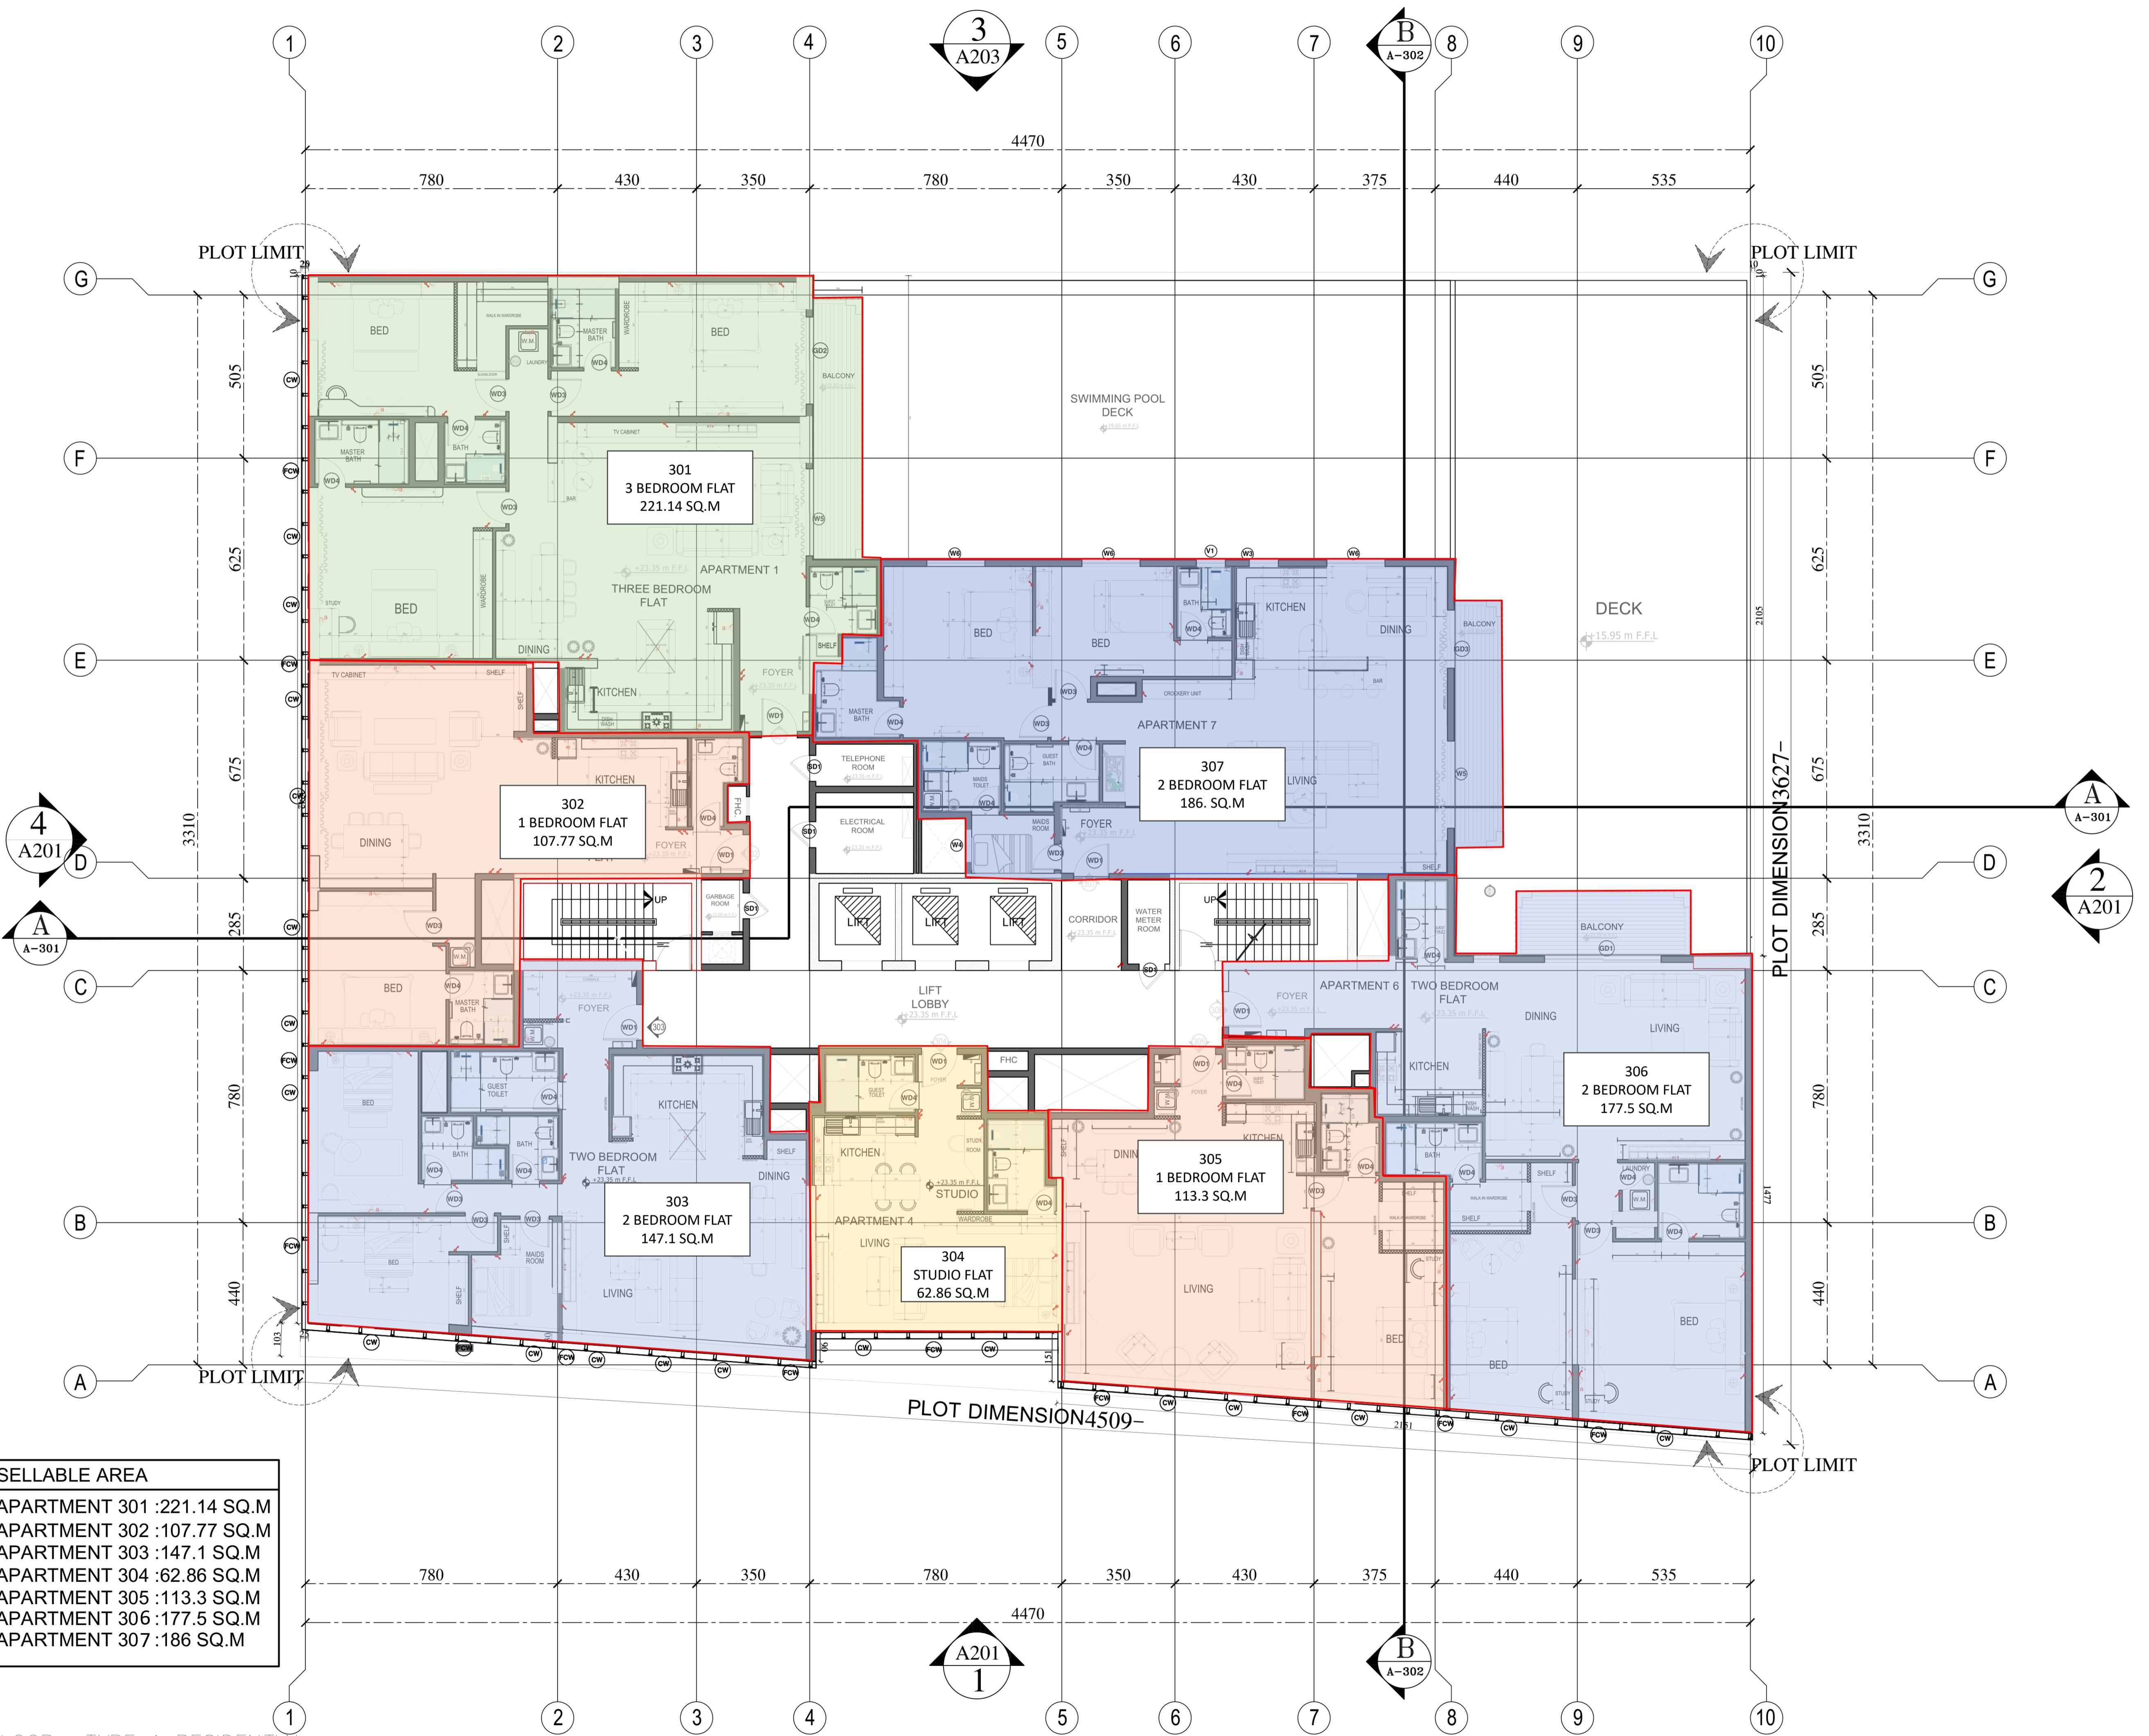



NOTES:-

- (1) THIS DRAWING IS THE PROPERTY OF : BARAJEEL ENGINEERING CONSULTANTS P.O.BOX 14496, DUBAI, U.A.E. IT IS NOT ALLOWED TO REPRODUCE ITS CONTENTS IN ANY FORM EXCEPT FOR THE PURPOSE FOR WHICH IT IS NEEDED.
- (2) THIS DRAWING IS NOT TO BE SCALED. STATED DIMENSIONS ONLY ARE TO BE CONSIDERED.
- (3) ANY DISCREPANCIES ARE TO BE BROUGHT TO THE ATTENTION OF THE ENGINEER AND RESOLVED BEFORE COMMENCEMENT OF ANY WORK.
- (4) ALL DIMENSIONS ARE IN CENTIMETERS.

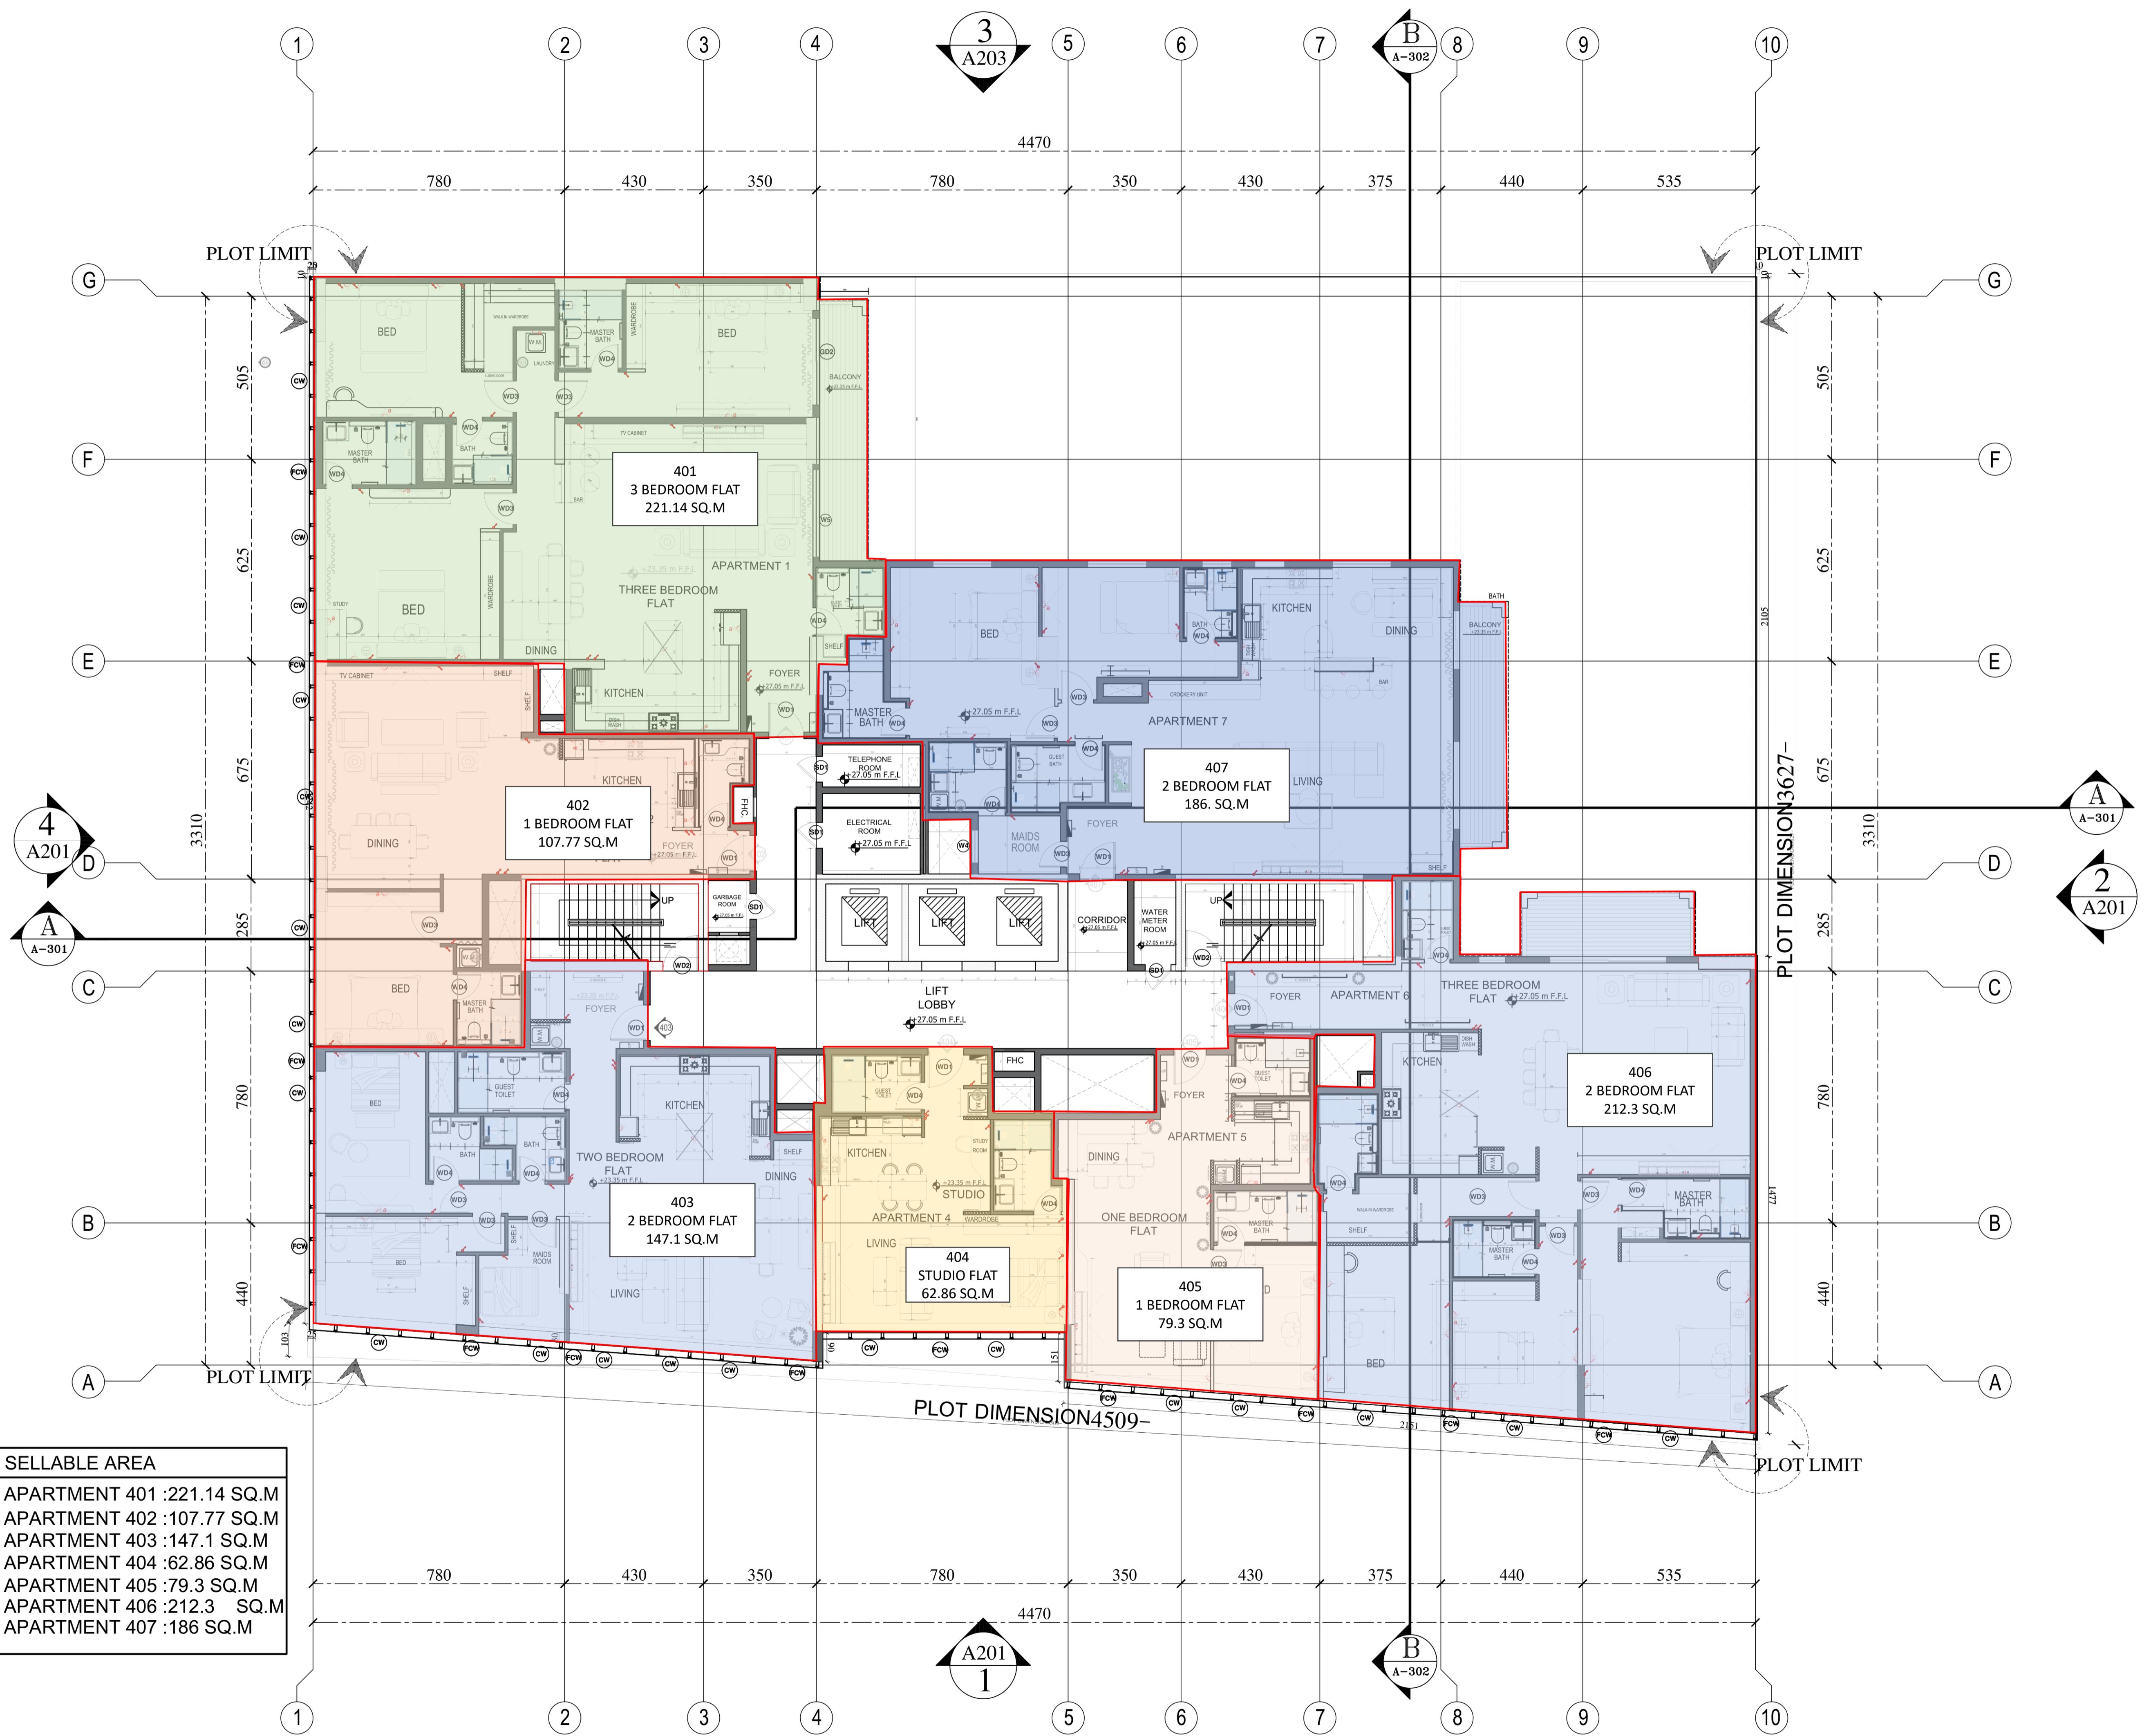

No:	DESCRIPTION	DATE	SIGN
PLOT:	JVC10WMR001	LOCATION:	JUMEIRA VILLAGE CIRCLE
CLIENT:	KARIM MIRZAAGHA JAHED PARI		
CONSULTANT:	AL GAFRY		
CONTRACTOR:	ZENITH SMART CONTRACTING		
PROJECT:	Proposed Residential & Commercial Building Gr. + 3P. + 11 Floor + ROOF PLOT NO: JVC10WMR001, AL BARSHA SOUTH FOURTH		
STAGE:	ARCHITECTURAL		
DRAWING TITLE:	FOURTH-SEVENTH FLOOR RESIDENTIAL		
CAD FILE:			
SCALE	DATE	DRAWN BY	JOB NO.
N.T.S	DEC/2024		



NOTES:-

- (1) THIS DRAWING IS THE PROPERTY OF : BARAJEEL ENGINEERING CONSULTANTS P.O.BOX 14496, DUBAI, U.A.E. IT IS NOT ALLOWED TO REPRODUCE ITS CONTENTS IN ANY FORM EXCEPT FOR THE PURPOSE FOR WHICH IT IS NEEDED.
- (2) THIS DRAWING IS NOT TO BE SCALED. STATED DIMENSIONS ONLY ARE TO BE CONSIDERED.
- (3) ANY DISCREPANCIES ARE TO BE BROUGHT TO THE ATTENTION OF THE ENGINEER AND RESOLVED BEFORE COMMENCEMENT OF ANY WORK.
- (4) ALL DIMENSIONS ARE IN CENTIMETERS.



No: DESCRIPTION DATE SIGN

PLOT: JVC10WMR001 LOCATION: JUMEIRA VILLAGE CIRCLE

CLIENT: KARIM MIRZAAGHA JAHED PARI

CONSULTANT: AL GAFRY

AL GAFRY CONSULTING ARCHITECTS ENGINEERS
P.O.BOX NO-48347,Dubai,U.A.E
TELE:-+971 42678184,FAX NO.-971 42671881

CONTRACTOR: ZENITH SMART CONTRACTING
AL SHAFAR TOWER 1,TECOM
BARSHA,DUBAI-P.O.BOX.125180
P.O.Box:125180 DUBAI Tel: 043688588 FAX:043688424


PROJECT: Proposed Residential & Commercial Building
Gr. + 3P. + 11 Floor + ROOF
PLOT NO: JVC10WMR001, AL BARSHA SOUTH FOURTH

STAGE: ARCHITECTURAL

DRAWING TITLE: EIGHTH-TENTH FLOOR RESIDENTIAL

CAD FILE:

SCALE	DATE	DRAWN BY	JOB NO.
N.T.S	JAN/2025		

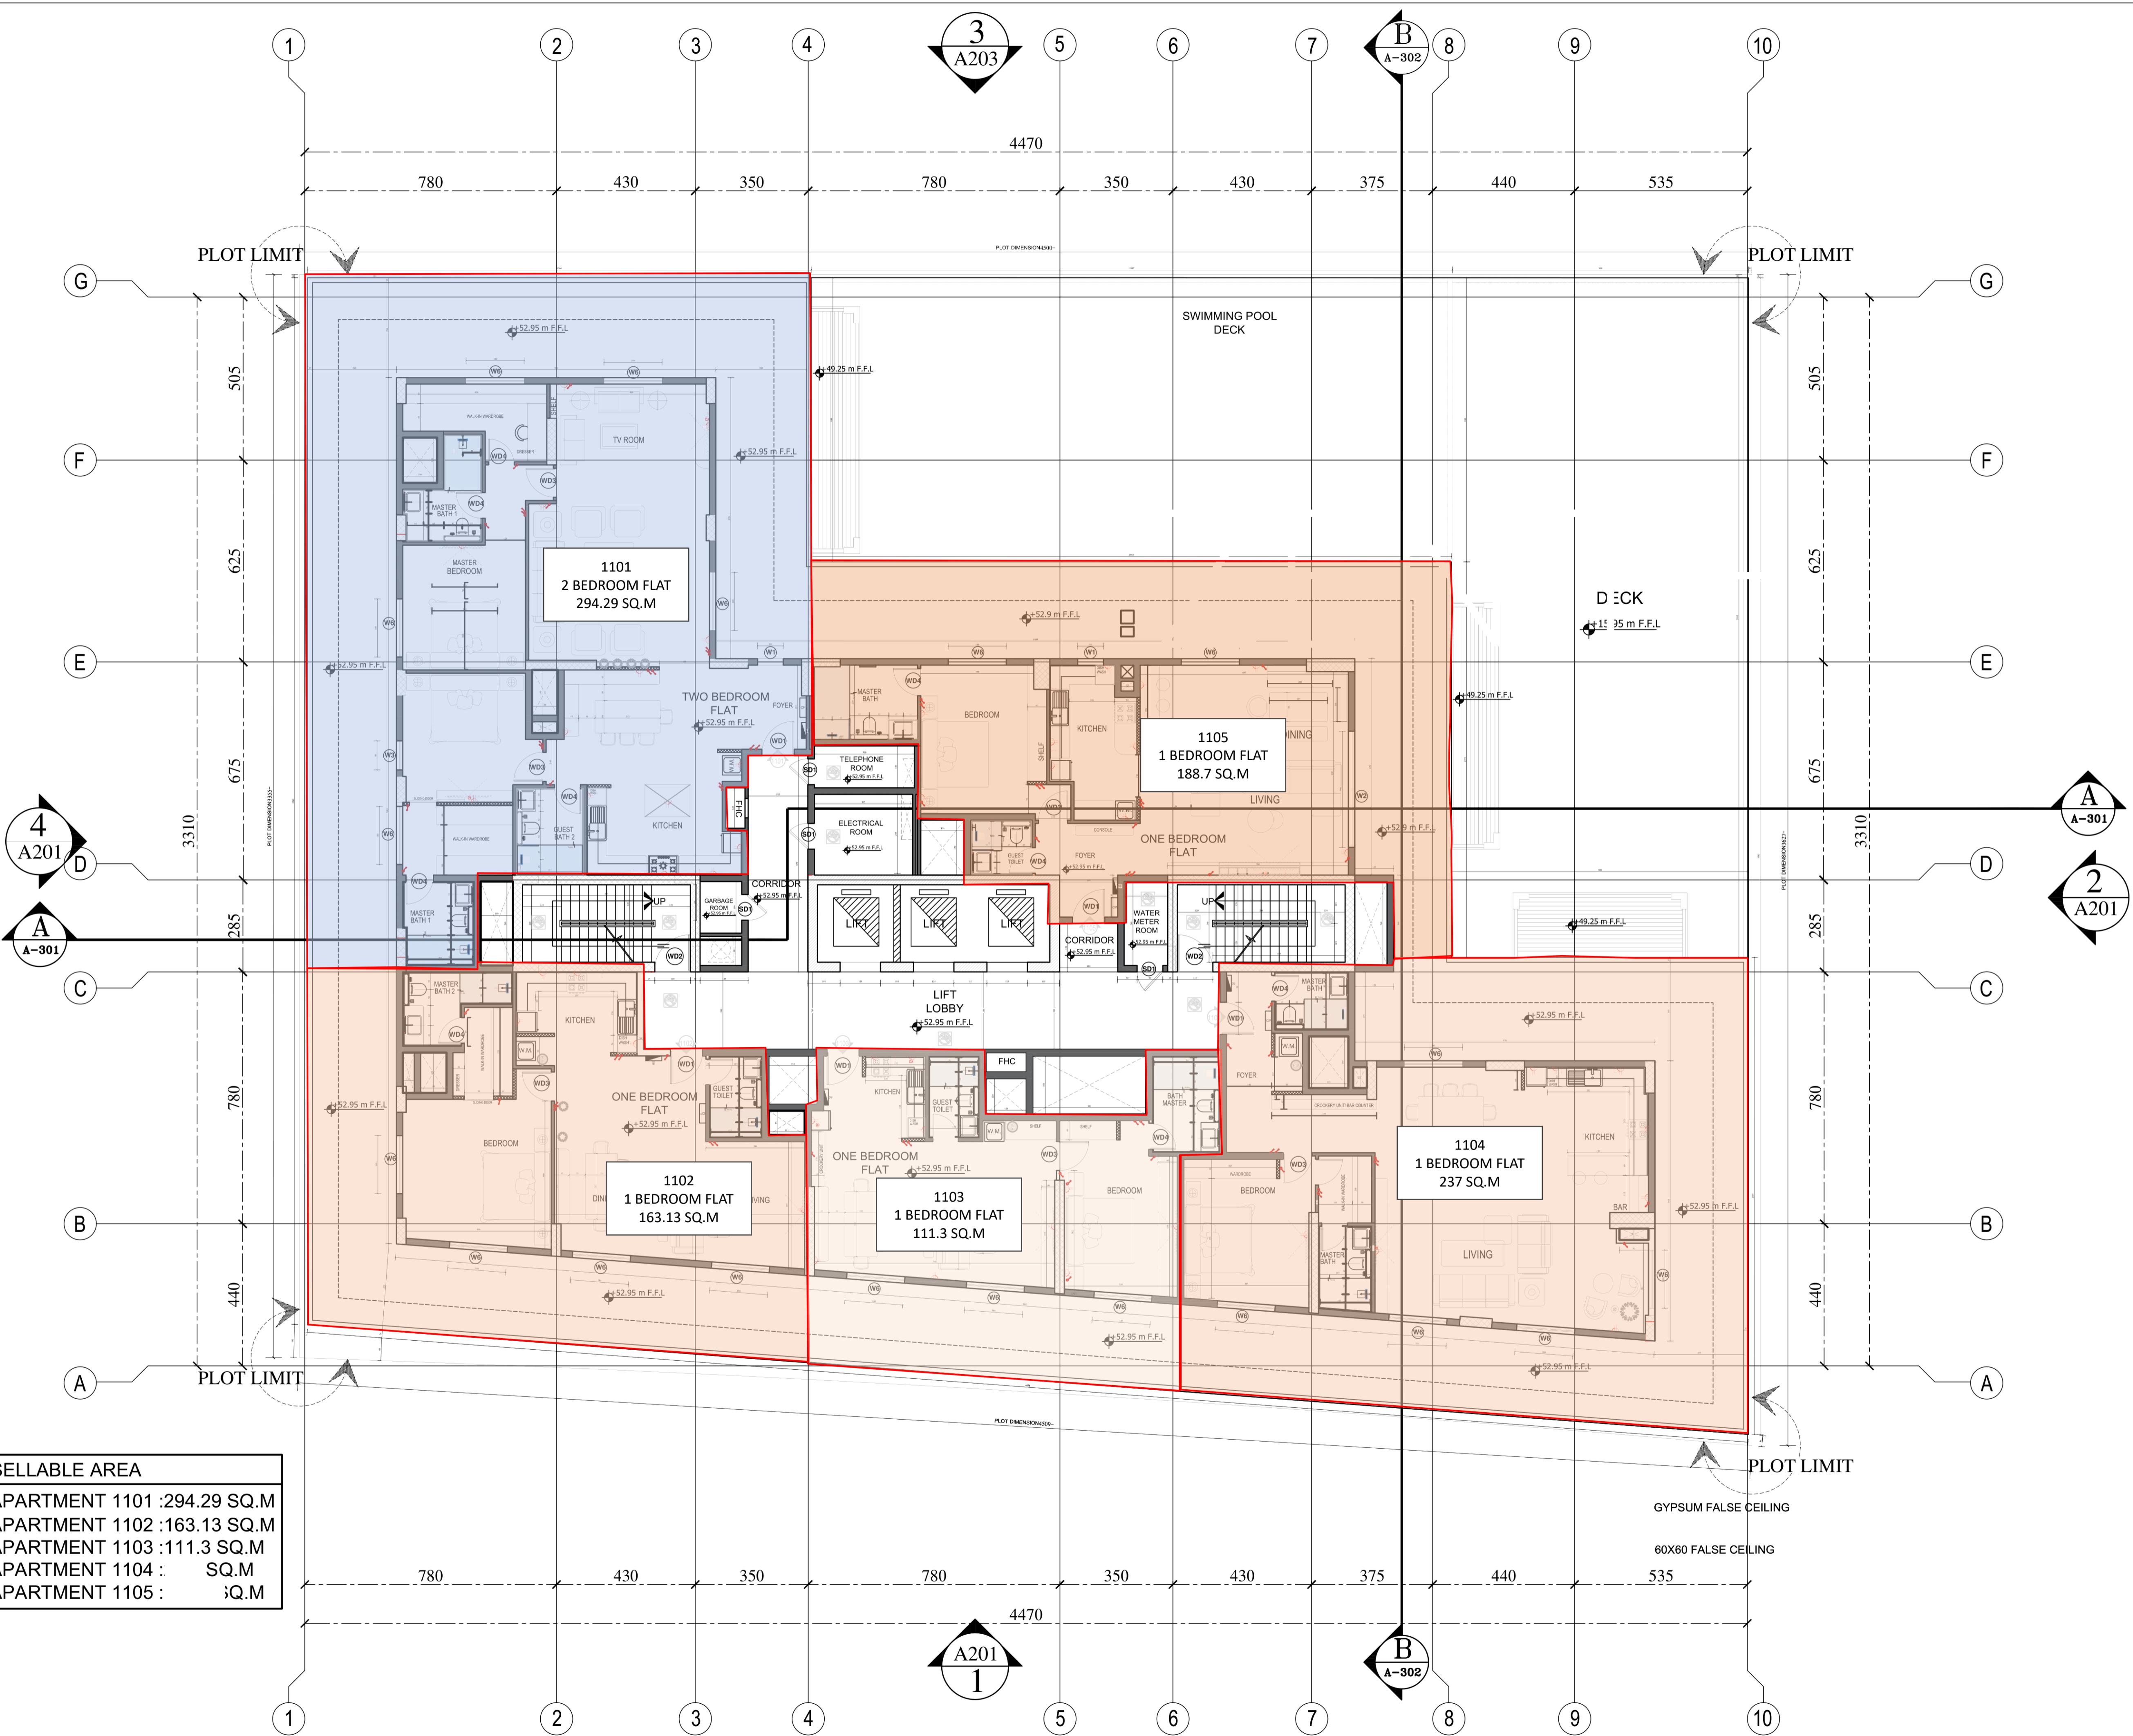


No:	DESCRIPTION	DATE	SIGN
PLOT: JVC10WMR001 LOCATION: JUMEIRA VILLAGE CIRCLE			
CLIENT: KARIM MIRZAAGHA JAHED PARI			
CONSULTANT: AL GAFRY			
CONTRACTOR: ZENITH SMART CONTRACTING			
PROJECT: Proposed Residential & Commercial Building Gr. + 3P. + 11 Floor + ROOF			
STAGE: ARCHITECTURAL			
DRAWING TITLE: ELEVENTH FLOOR RESIDENTIAL			
CAD FILE:			
SCALE	DATE	DRAWN BY	JOB NO.
N.T.S	JAN 2025		



NOTES:-

- (1) THIS DRAWING IS THE PROPERTY OF : BARAJEEL ENGINEERING CONSULTANTS P.O.BOX 14496, DUBAI, U.A.E. IT IS NOT ALLOWED TO REPRODUCE ITS CONTENTS IN ANY FORM EXCEPT FOR THE PURPOSE FOR WHICH IT IS NEEDED.
- (2) THIS DRAWING IS NOT TO BE SCALED. STATED DIMENSIONS ONLY ARE TO BE CONSIDERED.
- (3) ANY DISCREPANCIES ARE TO BE BROUGHT TO THE ATTENTION OF THE ENGINEER AND RESOLVED BEFORE COMMENCEMENT OF ANY WORK.
- (4) ALL DIMENSIONS ARE IN CENTIMETERS.

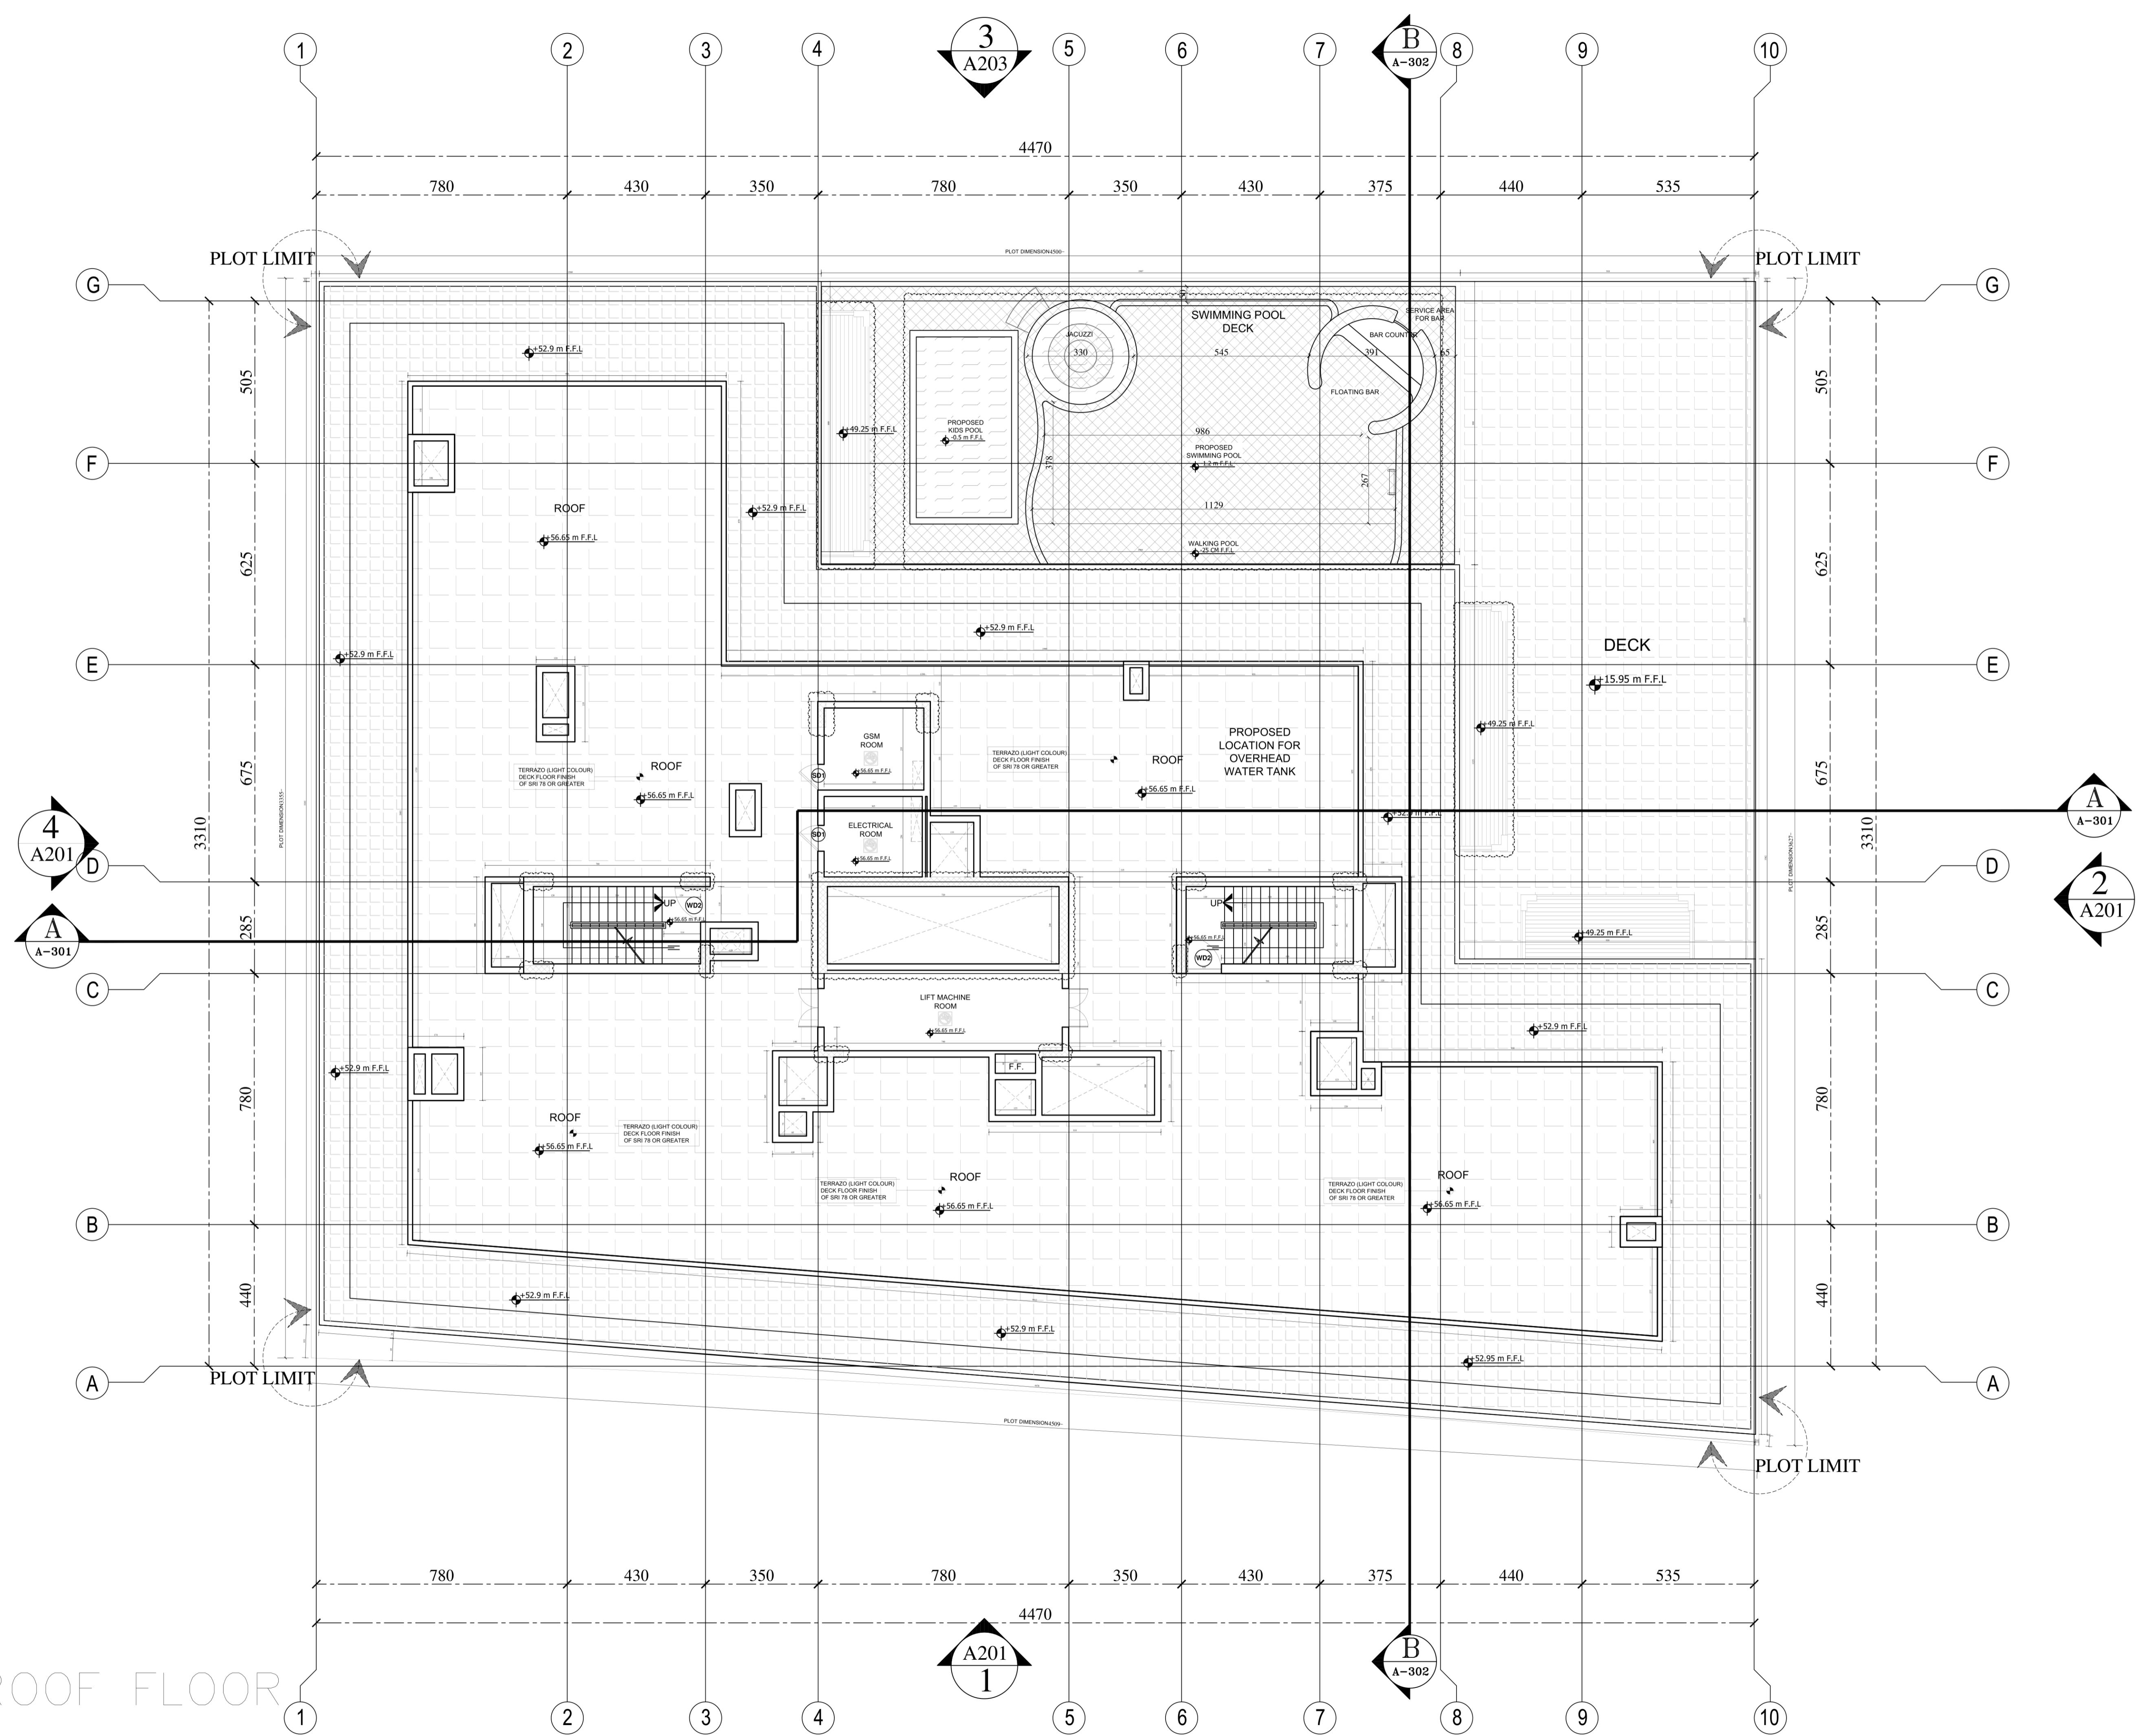

No:	DESCRIPTION	DATE	SIGN
PLOT:	JVC10WMRM001	LOCATION:	JUMEIRA VILLAGE CIRCLE
CLIENT:	KARIM MIRZAAGHA JAHED PARI		
CONSULTANT:	AL GAFRY		
	AL GAFRY CONSULTING ARCHITECTS ENGINEERS P.O.BOX NO-48347,Dubai,U.A.E TELE:-+971 42678184,FAX NO.-+971 426711881		
CONTRACTOR:	ZENITH SMART CONTRACTING		
	AL SHAFAR TOWER 1,TECOM BARSHA,DUBAI-P.O.BOX.125180 P.O.Box:125180 DUBAI Tel: 043688588 FAX:043688424		
PROJECT:	Proposed Residential & Commercial Building Gr. + 3P. + 11 Floor + ROOF PLOT NO: JVC10WMRM001, AL BARSHA SOUTH FOURTH		
STAGE:	ARCHITECTURAL		
DRAWING TITLE:	ROOF PLAN		
CAD FILE:			
SCALE	DATE	DRAWN BY	JOB NO.
N.T.S	DEC/2024		



NOTES:-

- (1) THIS DRAWING IS THE PROPERTY OF :
BARAJEEL ENGINEERING CONSULTANTS
P.O.BOX 14496, DUBAI, U.A.E.
IT IS NOT ALLOWED TO REPRODUCE ITS CONTENTS
IN ANY FORM EXCEPT FOR THE PURPOSE FOR
WHICH IT IS NEEDED.
- (2) THIS DRAWING IS NOT TO BE SCALED. STATED
DIMENSIONS ONLY ARE TO BE CONSIDERED.
- (3) ANY DISCREPANCIES ARE TO BE BROUGHT TO
THE ATTENTION OF THE ENGINEER AND RESOLVED
BEFORE COMMENCEMENT OF ANY WORK.
- (4) ALL DIMENSIONS ARE IN CENTIMETERS.

No:	DESCRIPTION	DATE	SIGN
PLOT:	LOCATION:		
JVC10WMRM001	JUMEIRA VILLAGE CIRCLE		
CLIENT: KARIM MIRZAAGHA JAHED PARI			
CONSULTANT:  AL GAFRY الغافري <small>CONSULTING ARCHITECTS ENGINEERS P.O.BOX NO.:48347,Dubai,U.A.E TELE:-+971 42678181,FAX NO:-+971 42671881</small>			
CONTRACTOR: <input checked="" type="checkbox"/> ZENITH SMART CONTRACTING AL SHAFAR TOWER 1,TECOM BARSHA,DUBAI-P.O.BOX.125180 P.O.Box:125180 DUBAI. Tel: 043688588 FAX:043688424			
PROJECT: Proposed Residential & Commercial Building Gr. + 3P. + 11 Floor + ROOF PLOT NO: JVC10WMRM001, AL BARSHA SOUTH FOURTH			
STAGE: ARCHITECTURAL			
DRAWING TITLE: TOP ROOF PLAN			
CAD FILE:			
SCALE	DATE	DRAWN BY	JOB NO.
N.T.S	DEC/2024		

